

개정3 가로주택정비사업 신축공사

2026. 02. 12

사업명	과정3 가로주택정비사업
-----	--------------

설계개요

공 사 명		괴정3 가로주택정비사업				
대지위치		부산 사하구 괴정동 1077번지 일원				
대지면적	전체면적	9,846.400 m ²	(2,978.54평)			
	도로	0.000 m ²	(0.00평)			
	공동주택부지	9,846.400 m ²	(2,978.54평)			
지역,지구		제2종 일반주거지역, 상대보호구역				
건축면적		1,754.656 m ²	(530.78평)	건폐율	17.82%	(법정:60%)
연 면 적		38,655.660 m ²	(11,693.34평)	용적률산정연면적	22,248.302 m ²	(6,730.11평)
지상면적		22,248.302 m ²	(6,730.11평)	리모델링 완화 용적률 108/110	16.00%	85~90점미만
용 적 률		225.95%	(완화용적률:226%)	특별공급비율 완화 용적률 105/100	10.00%	신혼(10%),23세대
용 도		공동주택 및 부대시설				다자녀(5%),12세대
규 모		지하 4층, 지상 1~26층	최고높이 : 75.5m	완화용적률	200%(기존)+16%+10%=226%	
구 조		철근콘크리트구조, 혼합구조		리모델링 완화 높이	108/100	최종 : 118/100
난방방식		개별난방방식		일반주거지역에서 시행하는 가로주택정비사업 추가 높이완화 110/100		
도 로		12,10,8,6M 도로		공동주택 동 개수	101,102,103동(3개동)	

조경면적	법 정	1,476.96 m²	15.00%			
	계 획	2,015.57 m²	20.47%			
주차대수	전용면적	법정기준		법정대수	계획	비고
	아파트	전용60㎡이하	1/0.7대	83 대	155 대	환경친화적 자동차 16대 (법정:15대) 총주차대수가 100개 이상인 경우 급속충전시설 1기 이상 (2기설치)
		전용85㎡이하	1/85	13 대	141 대	
		전용85㎡초과	1/70	1 대	3 대	
		세대당	1대이상	230 대	299 대	
	근린생활시설	1/134㎡당		0.00 대	6 대	(법정주차대수 : 1.30대)
	계			230 대	305 대	장애인주차대수 : 14대
세 대 수	230세대	조합원 : 82세대		일반분양 : 113세대		신혼부부 : 23세대 다자녀 : 12세대

세대별분양면적

(단위:㎡)

구 분	세대수	세대비율	전용면적	주거공유면적	공급면적		기타공용	총공급면적	지하주차장	계		비 고
				현관,계단,벽체공유,ELEV.			기계,전기,관리사무소,경로당등					
59A TYPE	51	22.17%	59.960	22.790	82.750	(25.03평)	6.510	89.260	50.760	140.020	(42.36평)	
59B TYPE	68	29.57%	59.954	22.555	82.509	(24.96평)	6.510	89.019	50.760	139.779	(42.28평)	
59C TYPE	18	7.83%	59.960	23.271	83.230	(25.18평)	6.510	89.740	50.760	140.500	(42.50평)	
84 TYPE	92	40.00%	84.955	30.004	114.959	(34.78평)	9.220	124.179	71.920	196.099	(59.32평)	
139 TYPE	1	0.43%	139.524	50.843	190.368	(57.59평)	15.140	205.508	118.120	323.628	(97.90평)	
계	230	100.00%	16,169.508	5,926.086	22,095.594	(6,683.92평)	1,755.008	23,850.602	13,688.984	37,539.587	(11,355.72평)	

* NOTE : 상기안은 건축심의조건 및 인 · 허가시 협의중 면적등의 변경이 있을수 있음.

건물개요

(단위:㎡)

구 분	규 모	지상층면적	지하층면적	계
공동주택	지하4~지상26층	22,095.594	-	22,095.594
관리사무소	지하4,지하3층	-	202.933	202.933
경로당	지상1층	131.148	-	131.148
주민공동시설	지하3층		631.660	631.660
기계/전기실	지하4,지하2층	-	587.434	587.434
지하주차장	지하4~지하1층	-	13,688.984	13,688.984
세대창고	지하1층	-	180.274	180.274
경비실	지상1층	21.560		21.560
				0.000
분양면적계		22,248.302	15,291.285	37,539.587
근린생활시설	지하4,지하3층	-	1,116.073	1,116.073
합 계		22,248.302	16,407.358	38,655.660

부대복리시설개요

(단위:㎡)


구 분	법 정	계 획	비 고
관리사무소	10+(세대수-50)*0.05	19.00 m²	202.933
주민공동시설	세대당*2.5	575.00 m²	1,058.581
	어린이놀이터(150세대이상)		260.000 옥외
	주민공동시설		587.434
	주민운동시설(500세대이상)		80.000 옥외
	경로당(150세대이상)		131.148
공동경로당	기존면적 : 78.37㎡	계획	108.42 m² 복지시설

■ 층별개요

																							연 면적	건축 면적	비 고
용도별	동별	층수	지하4층	지하3층	지하2층	지하1층	지하층소계	1층	2층	3~14층	15층	16층	17~18층	19층	20층	21층	22층	23층	24층	25층	26층	지상층소계			
공 동 주 택	101동	1F~19,25F					0.000	84.859	386.897	4,642.768	386.897	386.897	773.795	386.897	219.157	219.157	219.157	219.157	219.157	187.313		8,332.110	8,332.110	609.910	
	102동	1F~14,20,26F					0.000	104.226	342.709	5,047.579	420.632	347.653	685.418	342.709	342.709	174.487	174.487	174.487	174.487	174.487	174.487	8,680.554	8,680.554	675.448	
	103동	1F~24F					0.000	42.313	219.157	2,629.888	219.157	219.157	438.315	219.157	219.157	219.157	219.157	219.157	219.157			5,082.931	5,082.931	316.591	
합 계			0.000	0.000	0.000	0.000	0.000	231.397	948.764	12,320.234	1,026.686	953.708	1,897.527	948.764	781.024	612.801	612.801	612.801	612.801	361.799	174.487	22,095.594	22,095.594	1,601.949	
부대 복리 시설	관리사무소	지하4,지하3층	79.251	123.682			202.933																202.933		
	경로당	지상1층					0.000	131.148														131.148	131.148	131.148	
	주민공동시설	지하3층		631.660			631.660																631.660		
	기계/전기실	지하4,지하2층	312.531		274.903		587.434																587.434		
	지하주차장	지하4~지하1층	535.517	279.306	6,442.130	6,432.031	13,688.984																13,688.984		
	경비실	지상1층					0.000	21.560														21.560	21.560	21.560	
	세대창고	지하1층				180.274	180.274																180.274		
	외부계단-1,2	지상1층																							
합 계			927.299	1,034.647	6,717.033	6,612.305	15,291.285	152.708														152.708	15,443.993	152.708	
근린 생활 시설	근린 생활시설	지하4,지하3층	508.926	218.288			727.214																727.214		
	주차장	지하4층	314.442				314.442																314.442		
	기타	지하4층	74.418				74.418																74.418		
	합 계		897.785	218.288			1,116.073																1,116.073		
총 계			1,825.084	1,252.936	6,717.033	6,612.305	16,407.358	384.105	948.764	12,320.234	1,026.686	953.708	1,897.527	948.764	781.024	612.801	612.801	612.801	612.801	361.799	174.487	22,248.302	38,655.660	1,754.656	

과정3
가로주택정비사업

* NOTE.

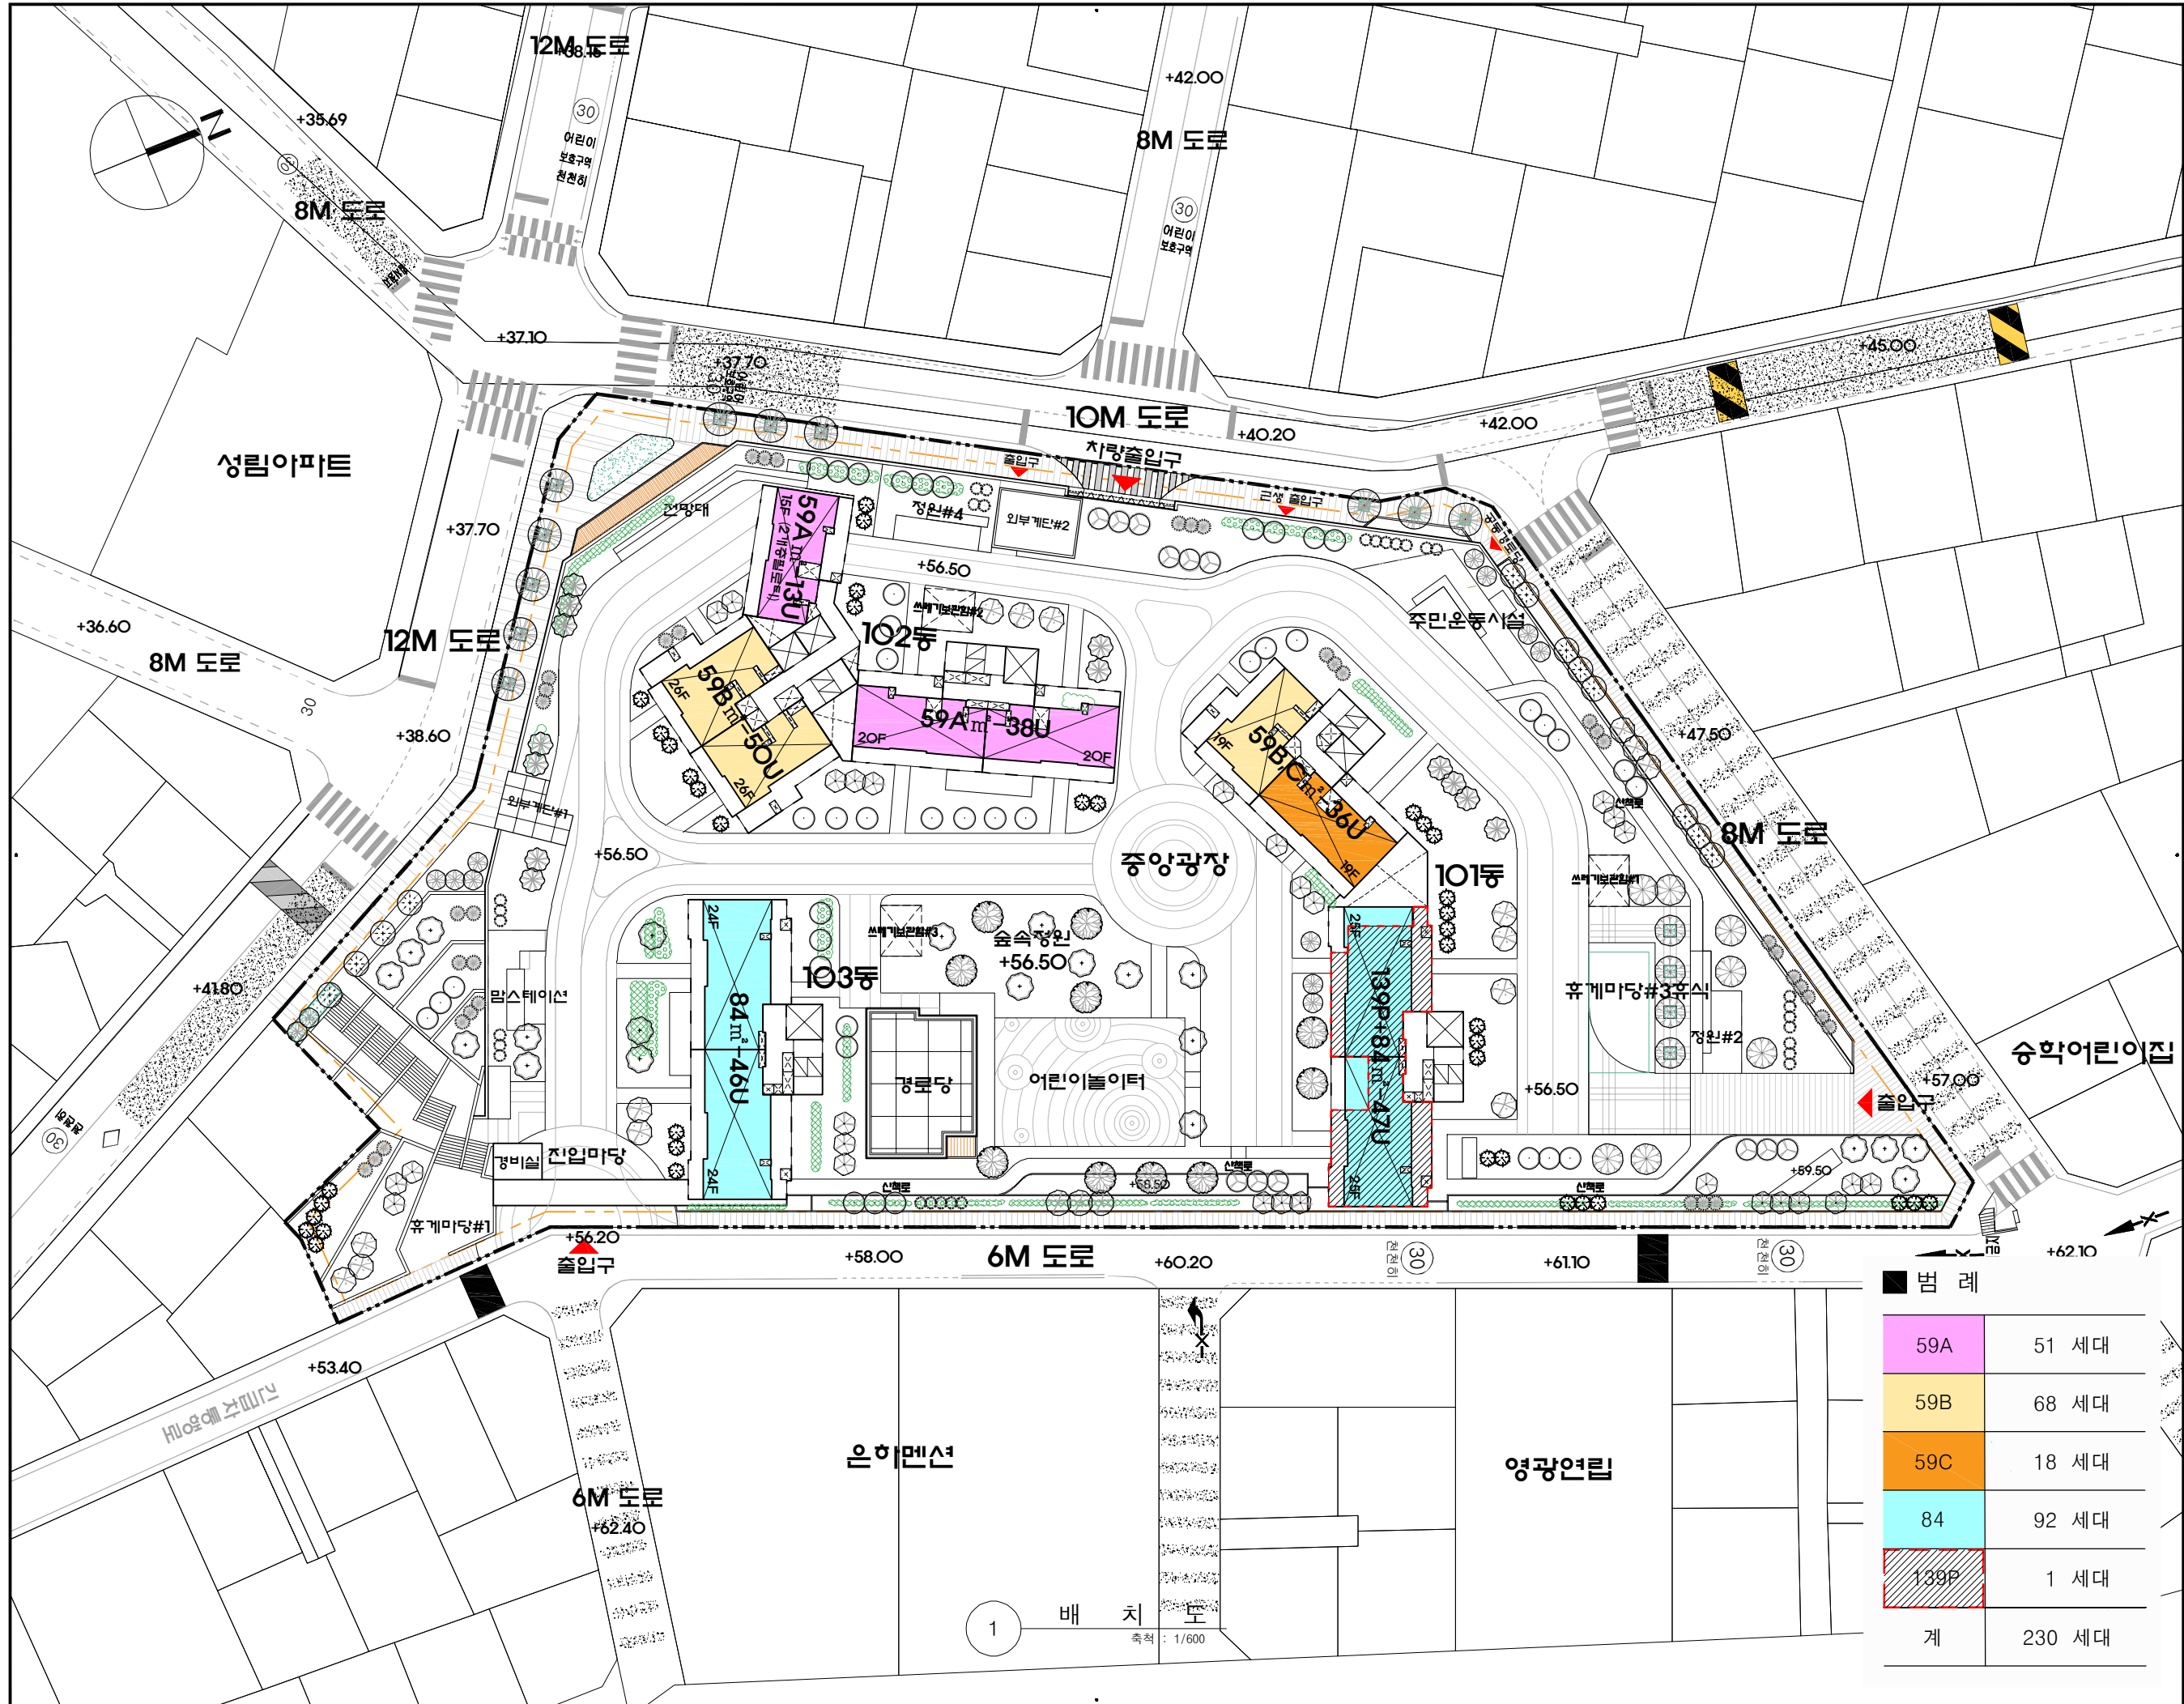

범례

59A	51 세대
59B	68 세대
59C	18 세대
84	92 세대
139P	1 세대
계	230 세대

1 배치도
축척 : 1/600

1					
0					
REV.	DATE	DESCRIPTION	BY	BY	APP.

SDglobal
I주ISD글로벌건축사무소
TEL/82-02-6956-9300 SEOUL, KOREA
서울시 성동구 독성로1길 31(성수동1가) 서울숲 M타워 308호

DRAWING TITLE
배치도


APPROVAL DATE 2025. 07.	APPROVED
PROJECT NO.	CHECKED 2
ENGINEER	CHECKED 1

SCALE A3: 1/600 A1: 1/300	DRAWN / DATE
DRAWING NO. 000	REV.

단위세대평면도

과정3
가로주택정비사업

* NOTE.

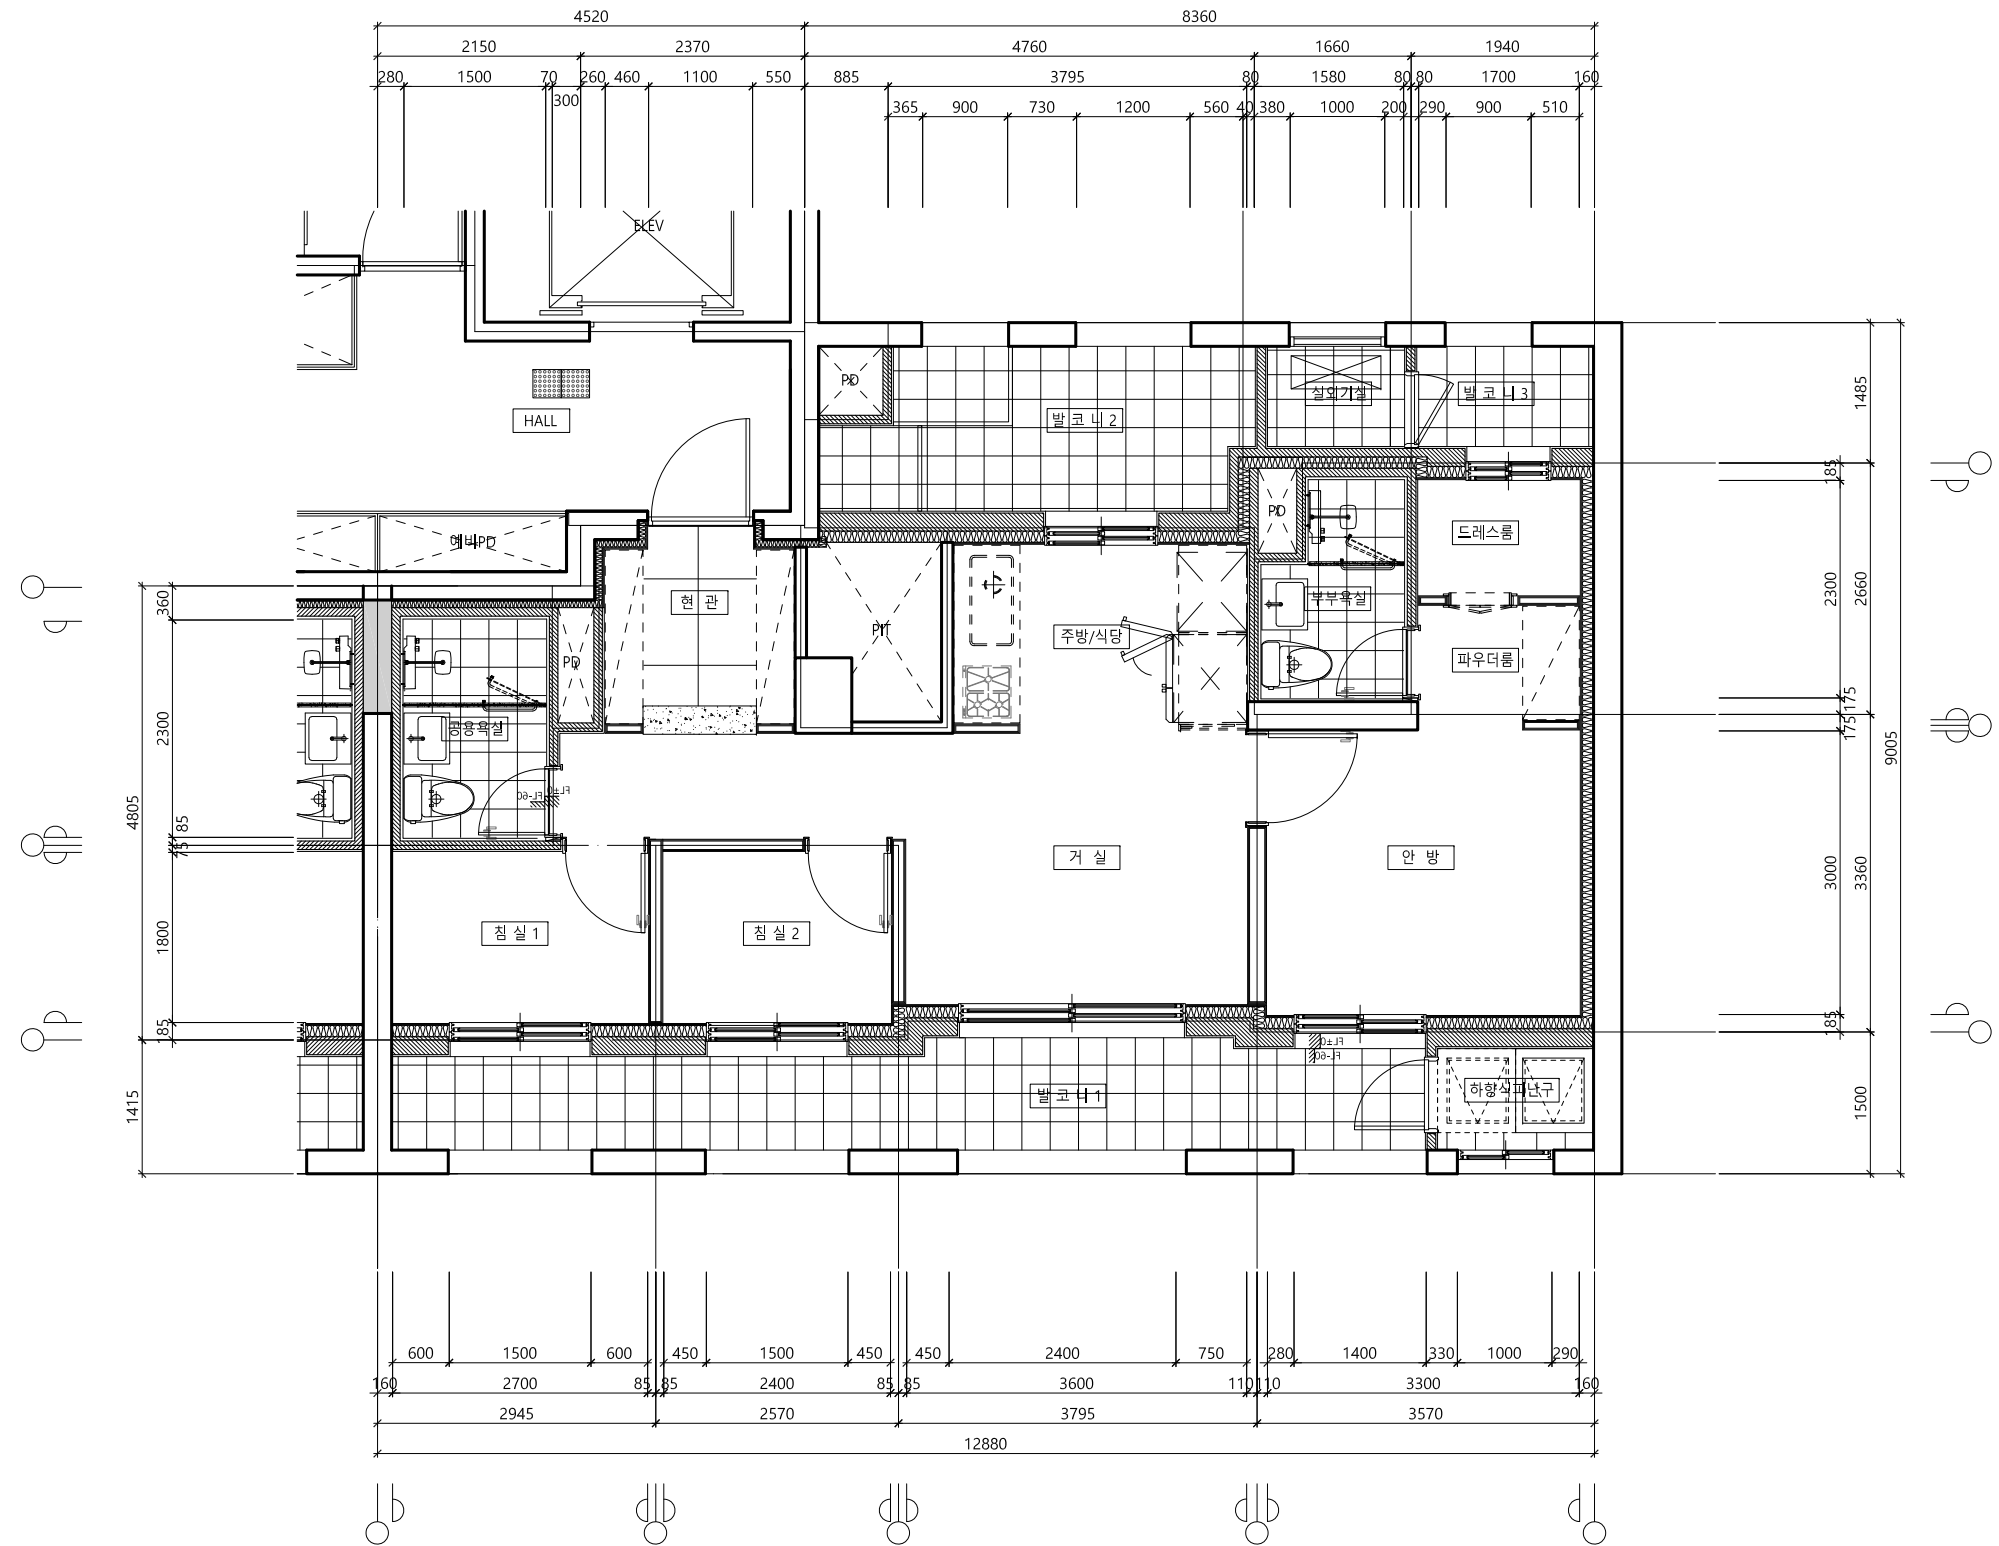

59Am² 단위세대평면도(기본형)
SCALE : A1= 1 / 40
A3= 1 / 80

1					
0					
REV.	DATE	DESCRIPTION	BY	BY	APP.

SDglobal


TEL/82-02-6956-9300 SEOUL, KOREA
서울시 성동구 독성로1길 31(성수동1가) 서울솔 M타워 308호

DRAWING TITLE
59Am² 단위세대평면도(기본형)

APPROVAL DATE 2025. 07.	APPROVED
PROJECT NO.	CHECKED 2
ENGINEER	CHECKED 1
SCALE A3: 1/ 80	A1: 1/ 40
DRAWING NO. A-000	REV.

과정3
가로주택정비사업

* NOTE.

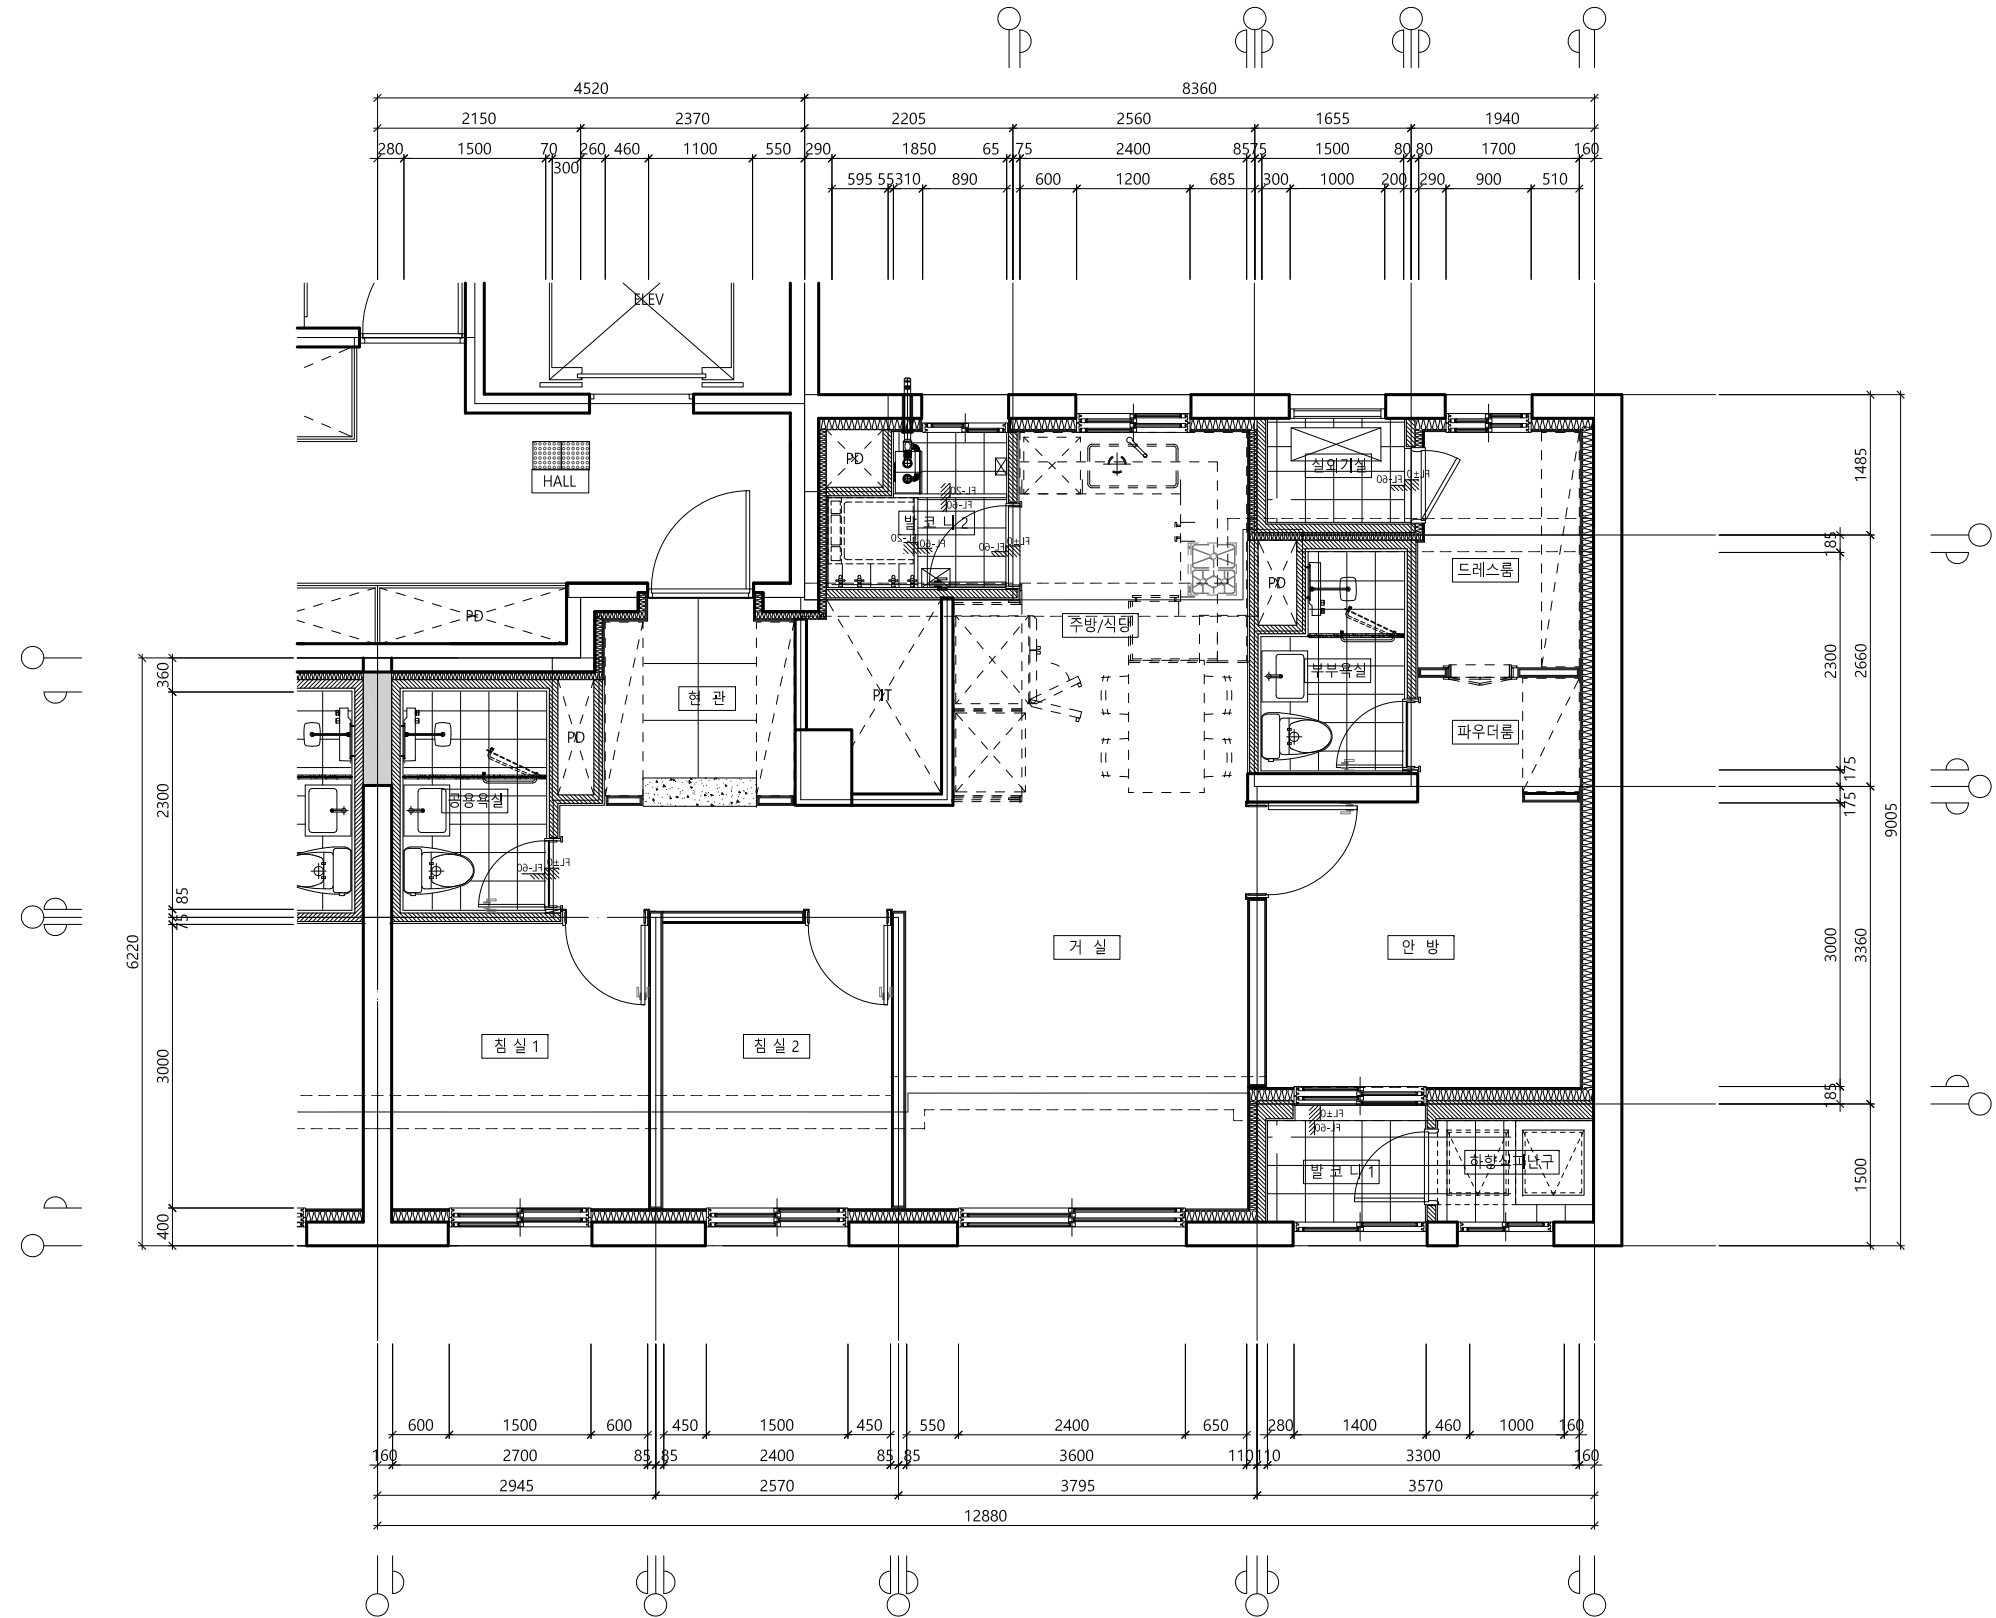

59A㎡ 단위세대평면도(확장형)

SCALE : A1= 1 / 40
A3= 1 / 80

1					
0					
REV.	DATE	DESCRIPTION	BY	BY	APP.

SDglobal


TEL/82-02-6956-9300 SEOUL, KOREA
서울시 성동구 독성로1길 31(성수동1가) 서울숲 M타워 308호

DRAWING TITLE
59A㎡ 단위세대평면도(확장형)

APPROVAL DATE 2025. 07.	APPROVED
PROJECT NO.	CHECKED 2
ENGINEER	CHECKED 1
SCALE A3: 1/ 80	A1: 1/ 40
DRAWING NO. A-000	REV.

과정3
가로주택정비사업

* NOTE.

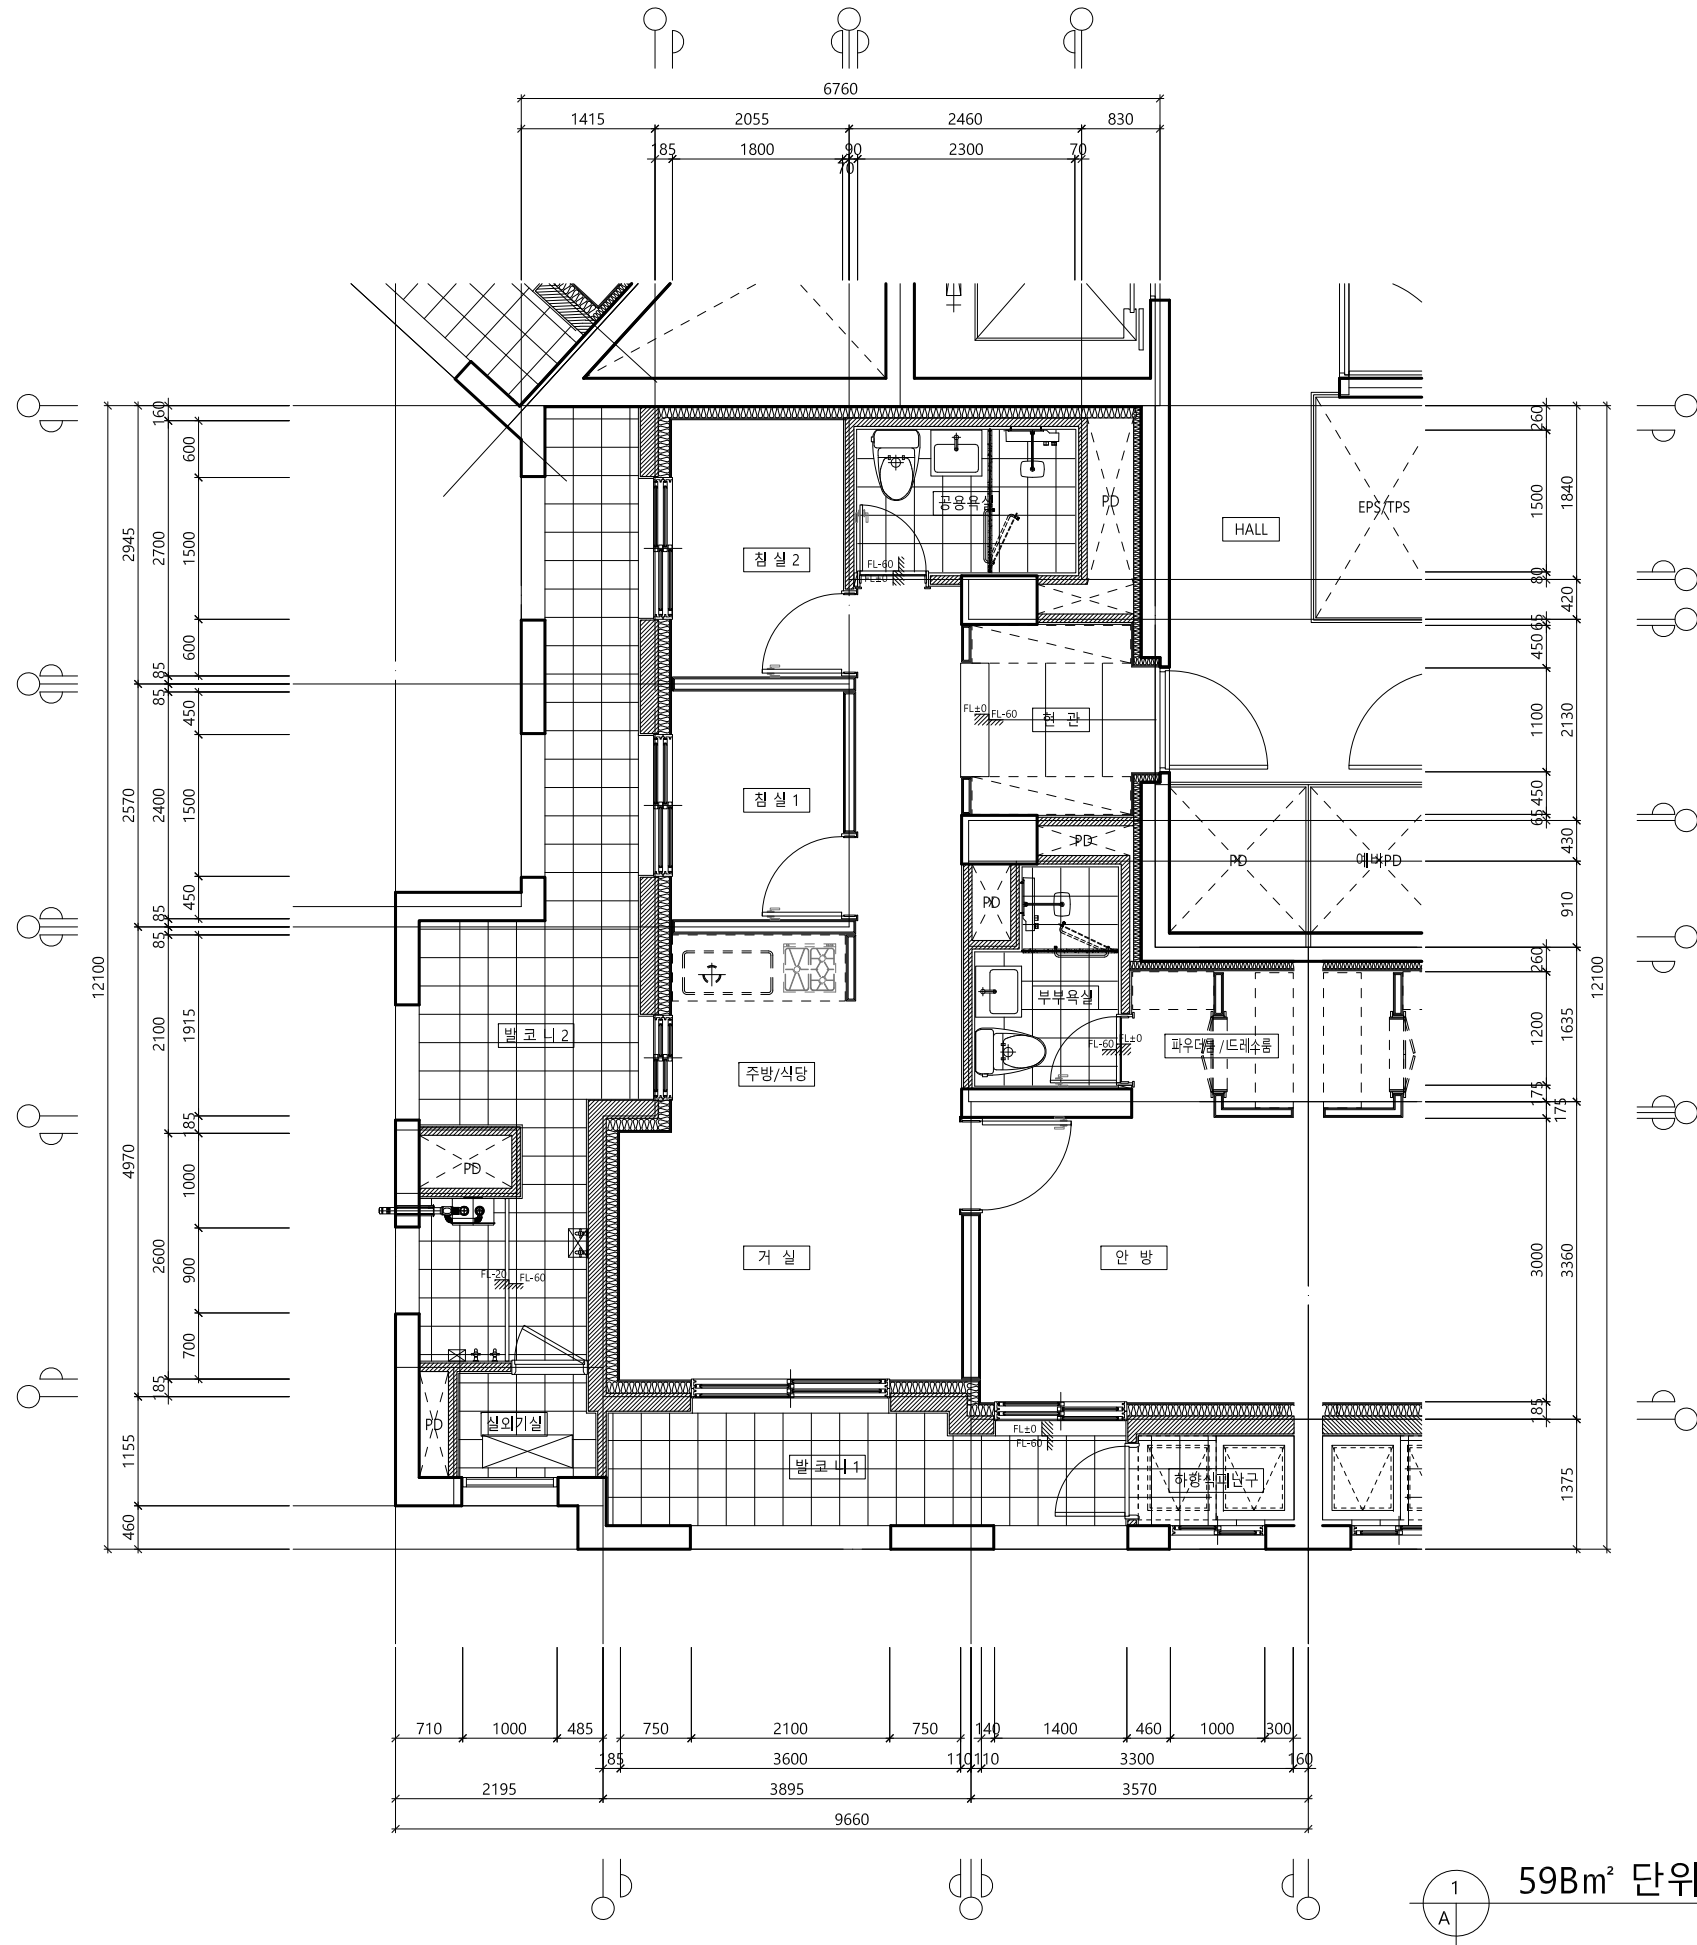

59Bm² 단위세대평면도(기본형)

SCALE : A1= 1 / 40
A3= 1 / 80

1					
0					
REV.	DATE	DESCRIPTION	BY	BY	APP.

SDglobal


TEL/82-02-6956-9300 SEOUL, KOREA
서울시 성동구 독성로1길 31(성수동1가) 서울을 M타워 308호

DRAWING TITLE
59Bm² 단위세대평면도(기본형)

APPROVAL DATE 2025. 07.	APPROVED
PROJECT NO.	CHECKED 2
ENGINEER	CHECKED 1
SCALE A3: 1/ 80 A1: 1/ 40	DRAWN / DATE
DRAWING NO. A-000	REV.

과정3
가로주택정비사업

* NOTE.

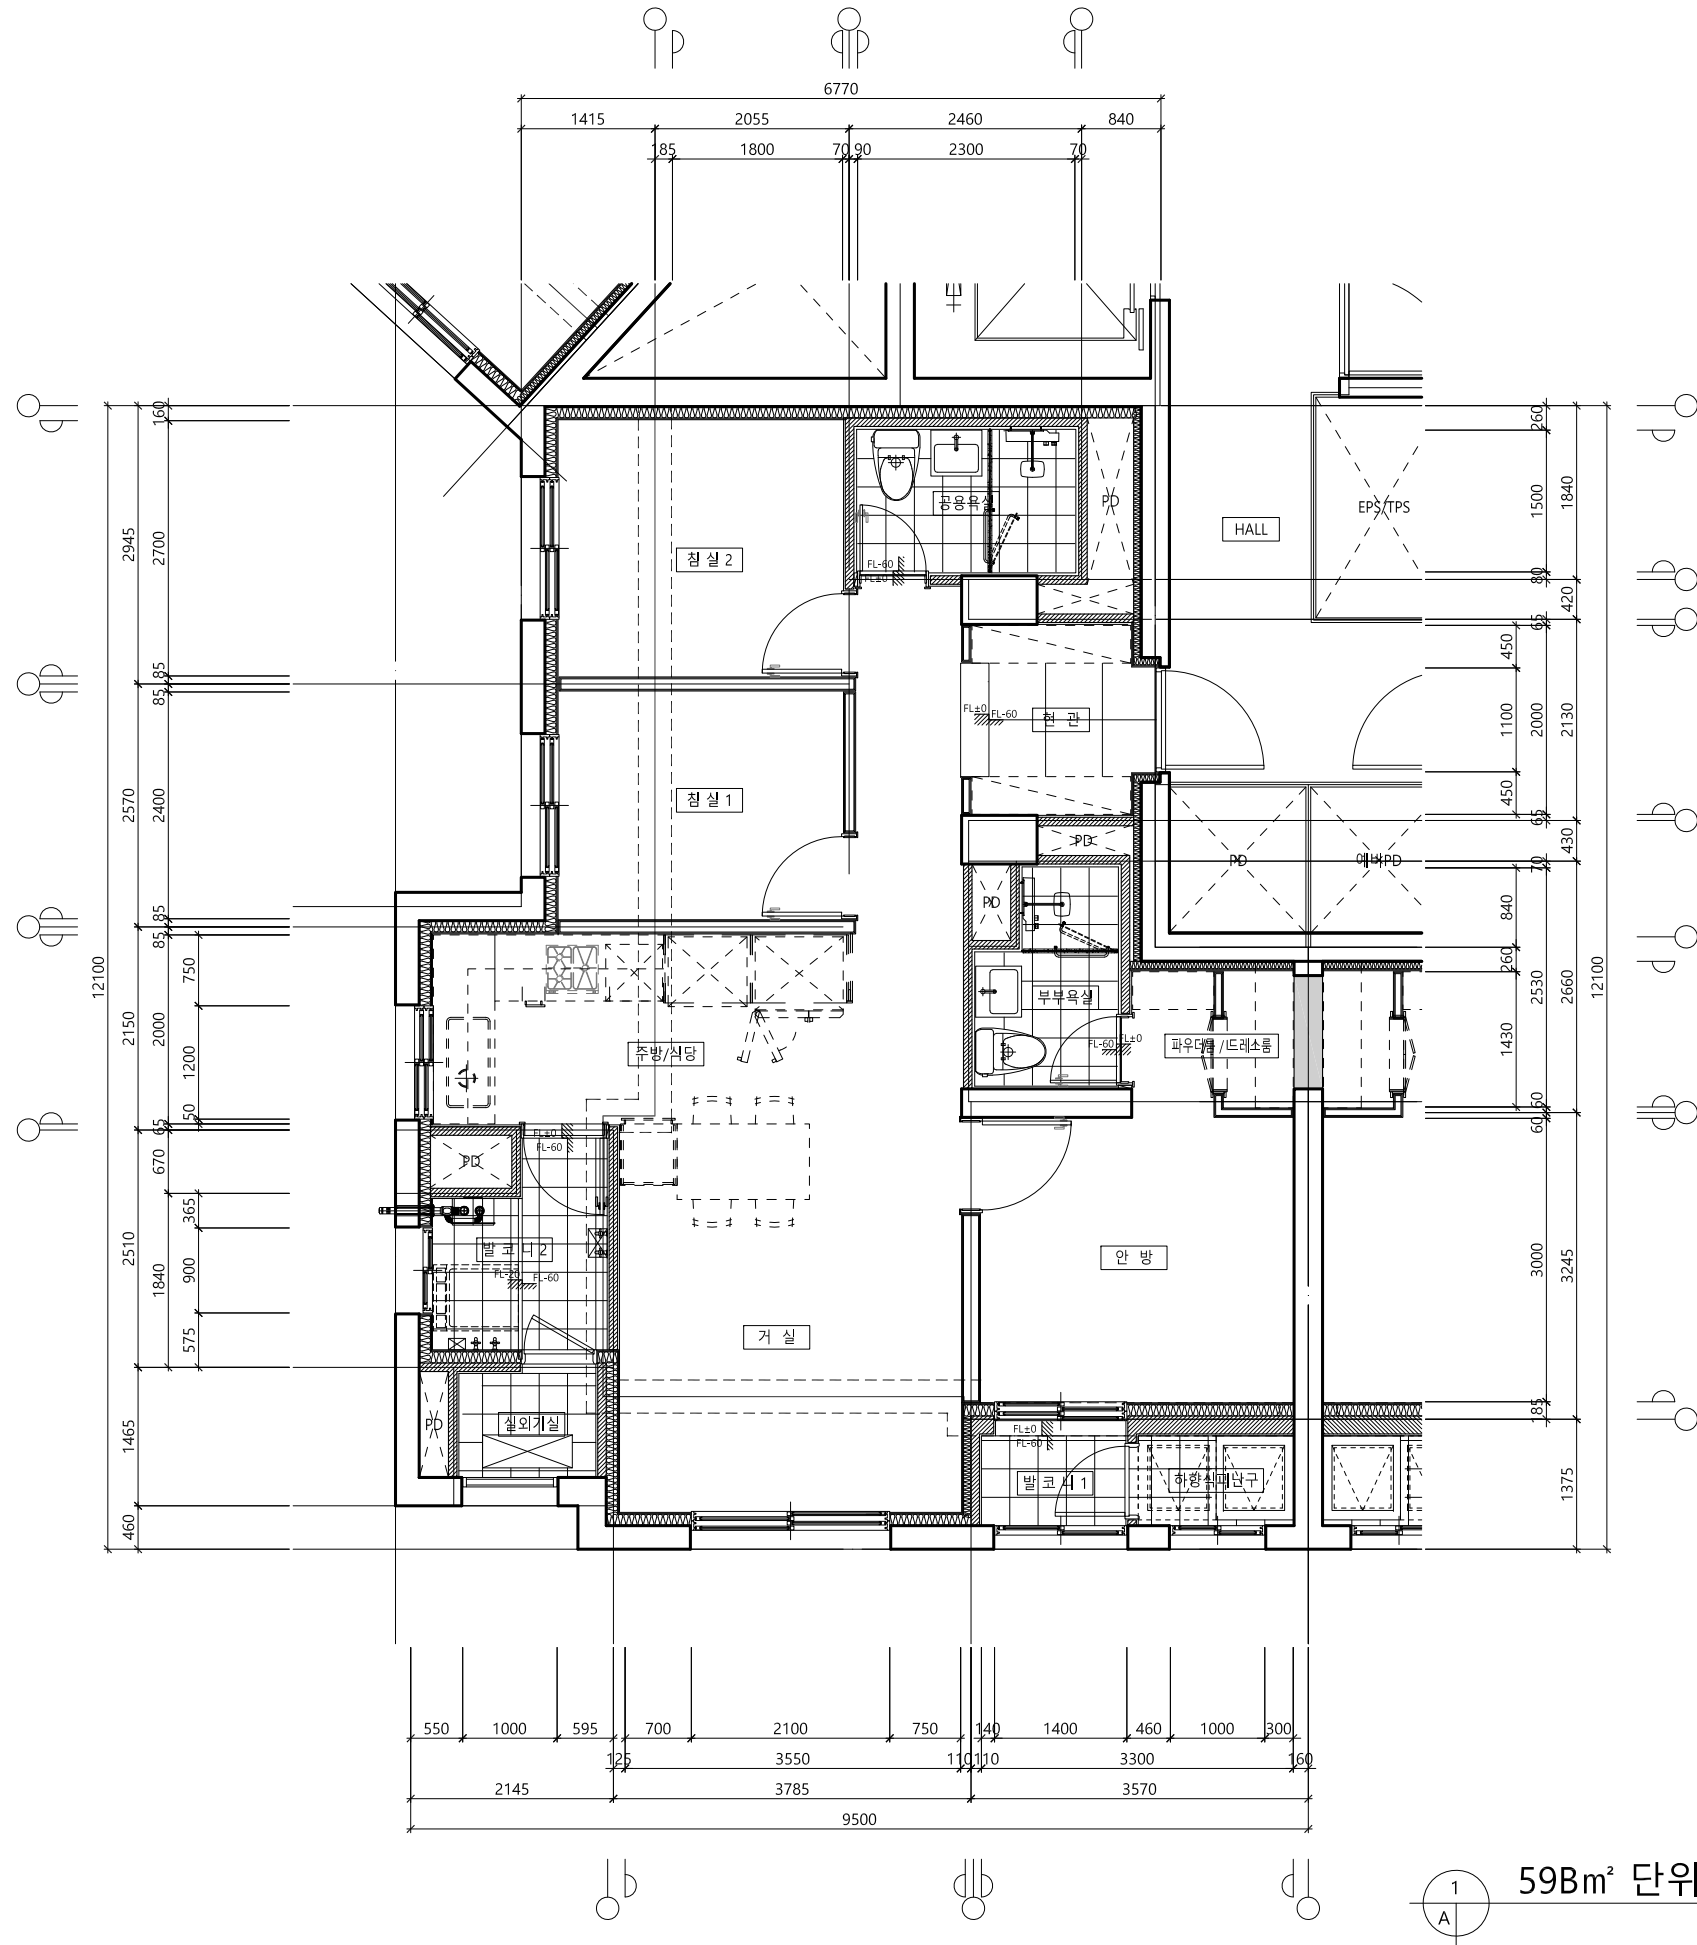

59Bm² 단위세대평면도(확장형)

SCALE : A1= 1 / 40
A3= 1 / 80

1					
0					
REV.	DATE	DESCRIPTION	BY	BY	APP.

SDglobal


TEL/82-02-6956-9300 SEOUL, KOREA
서울시 성동구 독성로1길 31(성수동1가) 서울을 M타워 308호

DRAWING TITLE
59Bm² 단위세대평면도(확장형)

APPROVAL DATE 2025. 07.	APPROVED
PROJECT NO.	CHECKED 2
ENGINEER	CHECKED 1
SCALE A3: 1/ 80 A1: 1/ 40	DRAWN / DATE
DRAWING NO. A-000	REV.

과정3
가로주택정비사업

* NOTE.

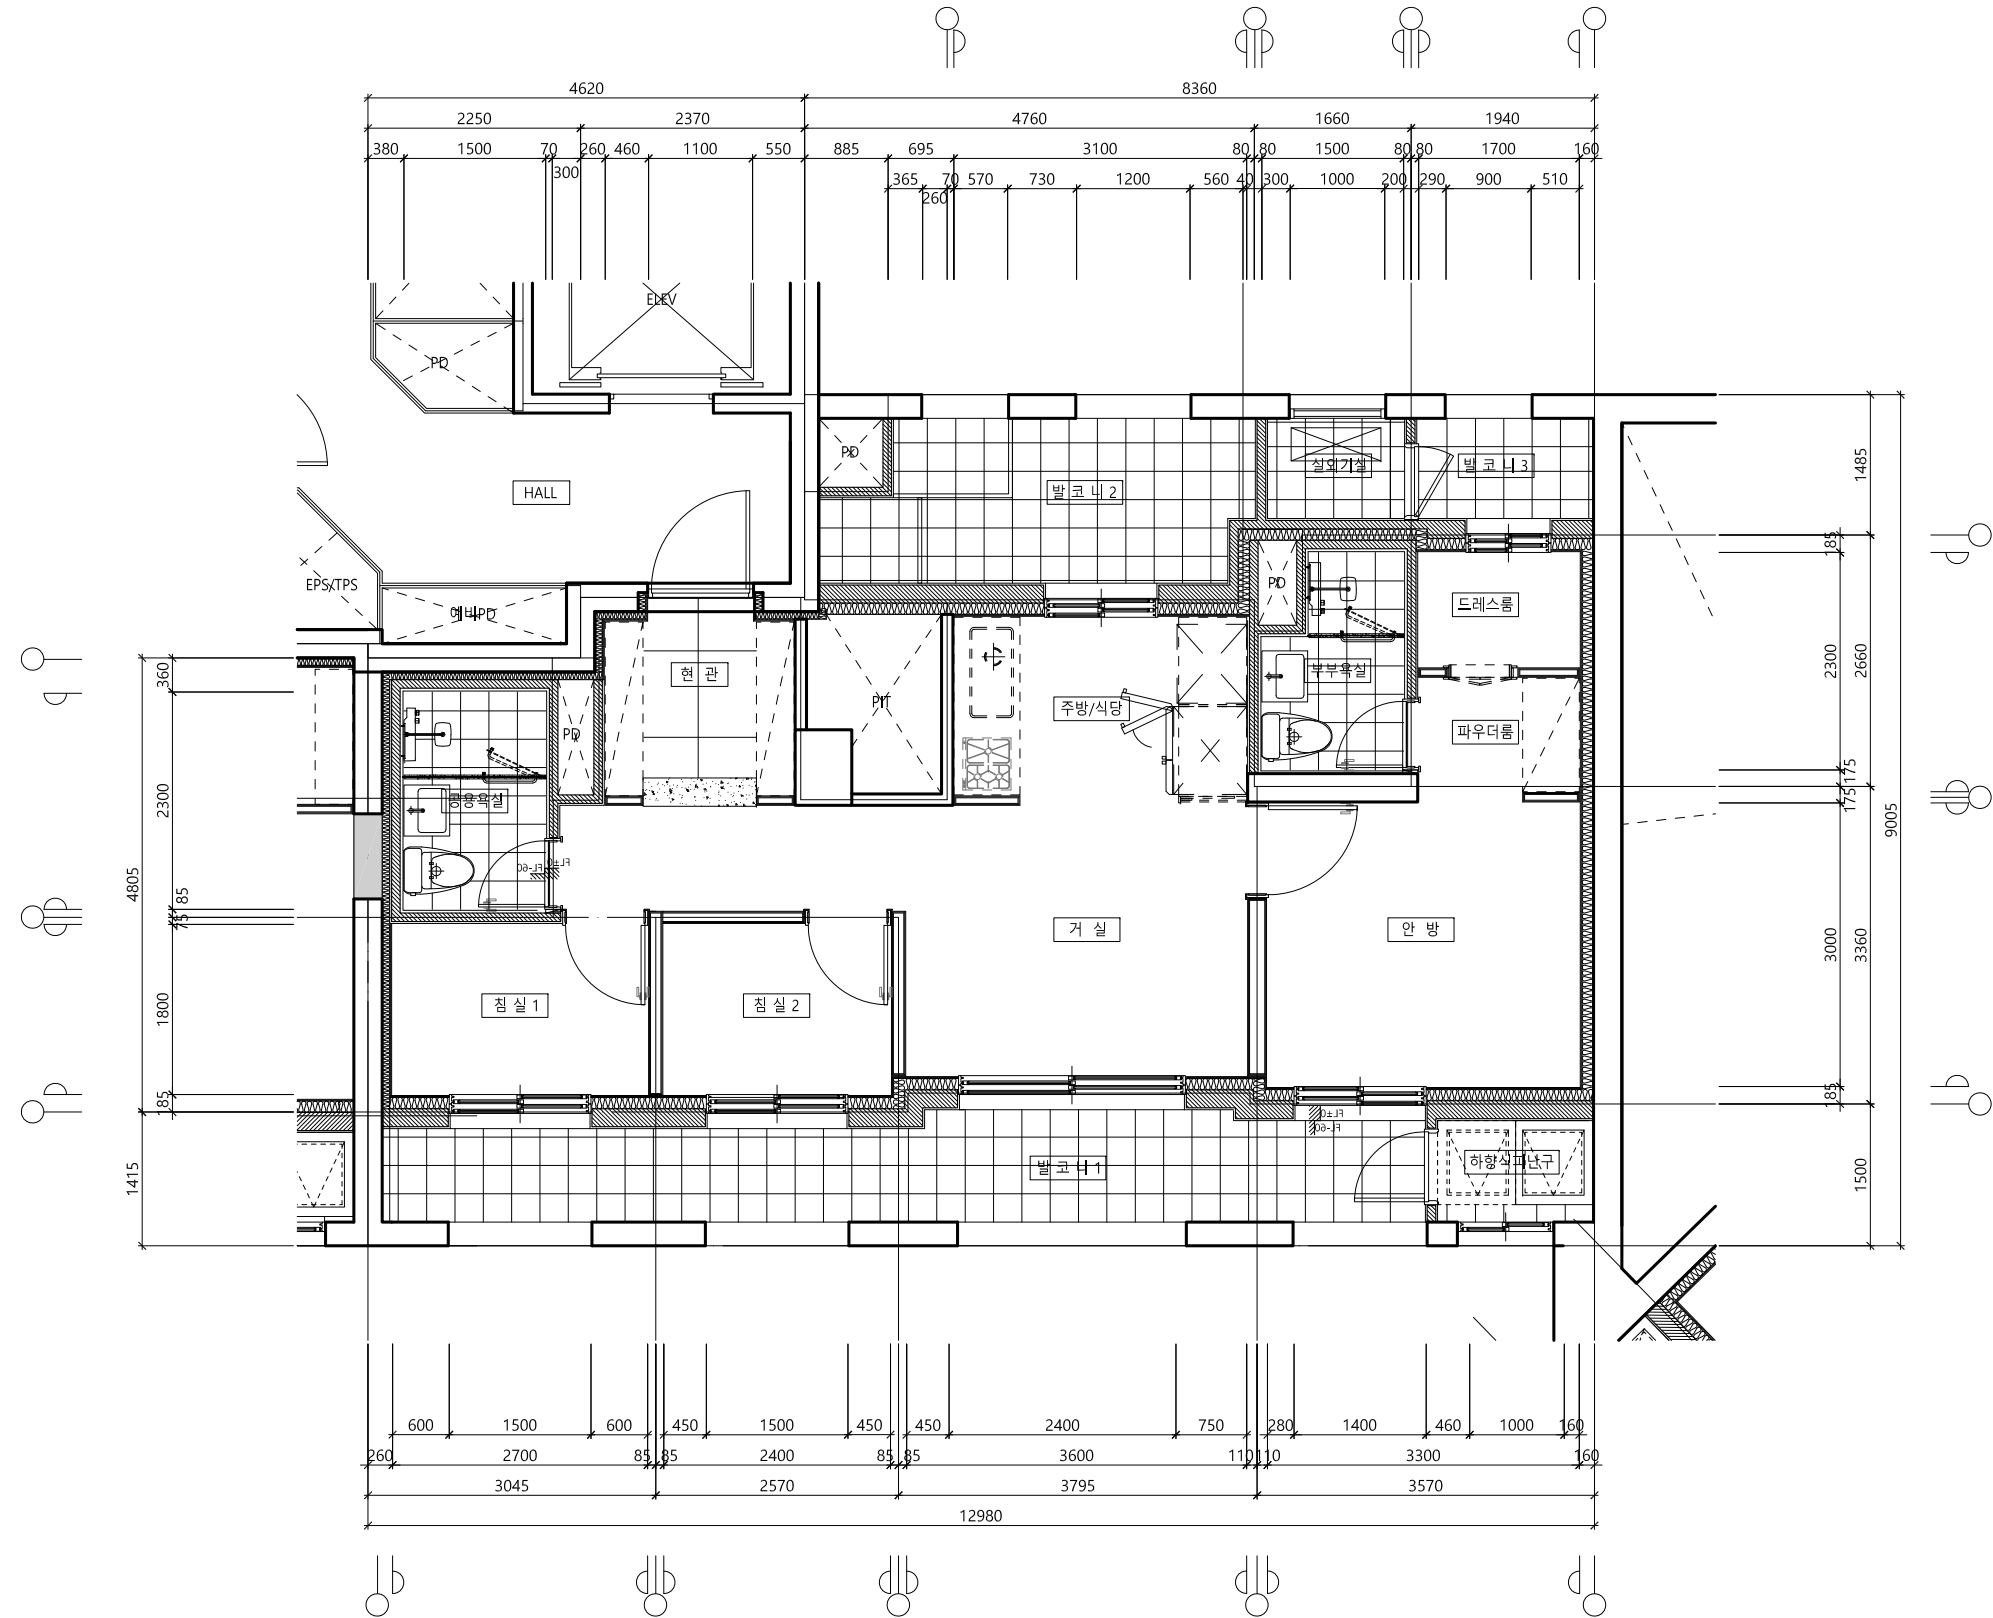

1
A

59Cm² 단위세대평면도(기본형)

SCALE : A1= 1 / 40
A3= 1 / 80

1					
0					
REV.	DATE	DESCRIPTION	BY	BY	APP.

SDglobal


I주SD글로벌건축사사무소
TEL/82-02-6956-9300 SEOUL, KOREA
서울시 성동구 독성로1길 31(성수동1가) 서울숲 M타워 308호

DRAWING TITLE
59Cm² 단위세대평면도(기본형)

APPROVAL DATE 2025. 07.	APPROVED
PROJECT NO.	CHECKED 2
ENGINEER	CHECKED 1
SCALE A3: 1/ 80	A1: 1/ 40
DRAWING NO. A-000	REV.

과정3
가로주택정비사업

* NOTE.

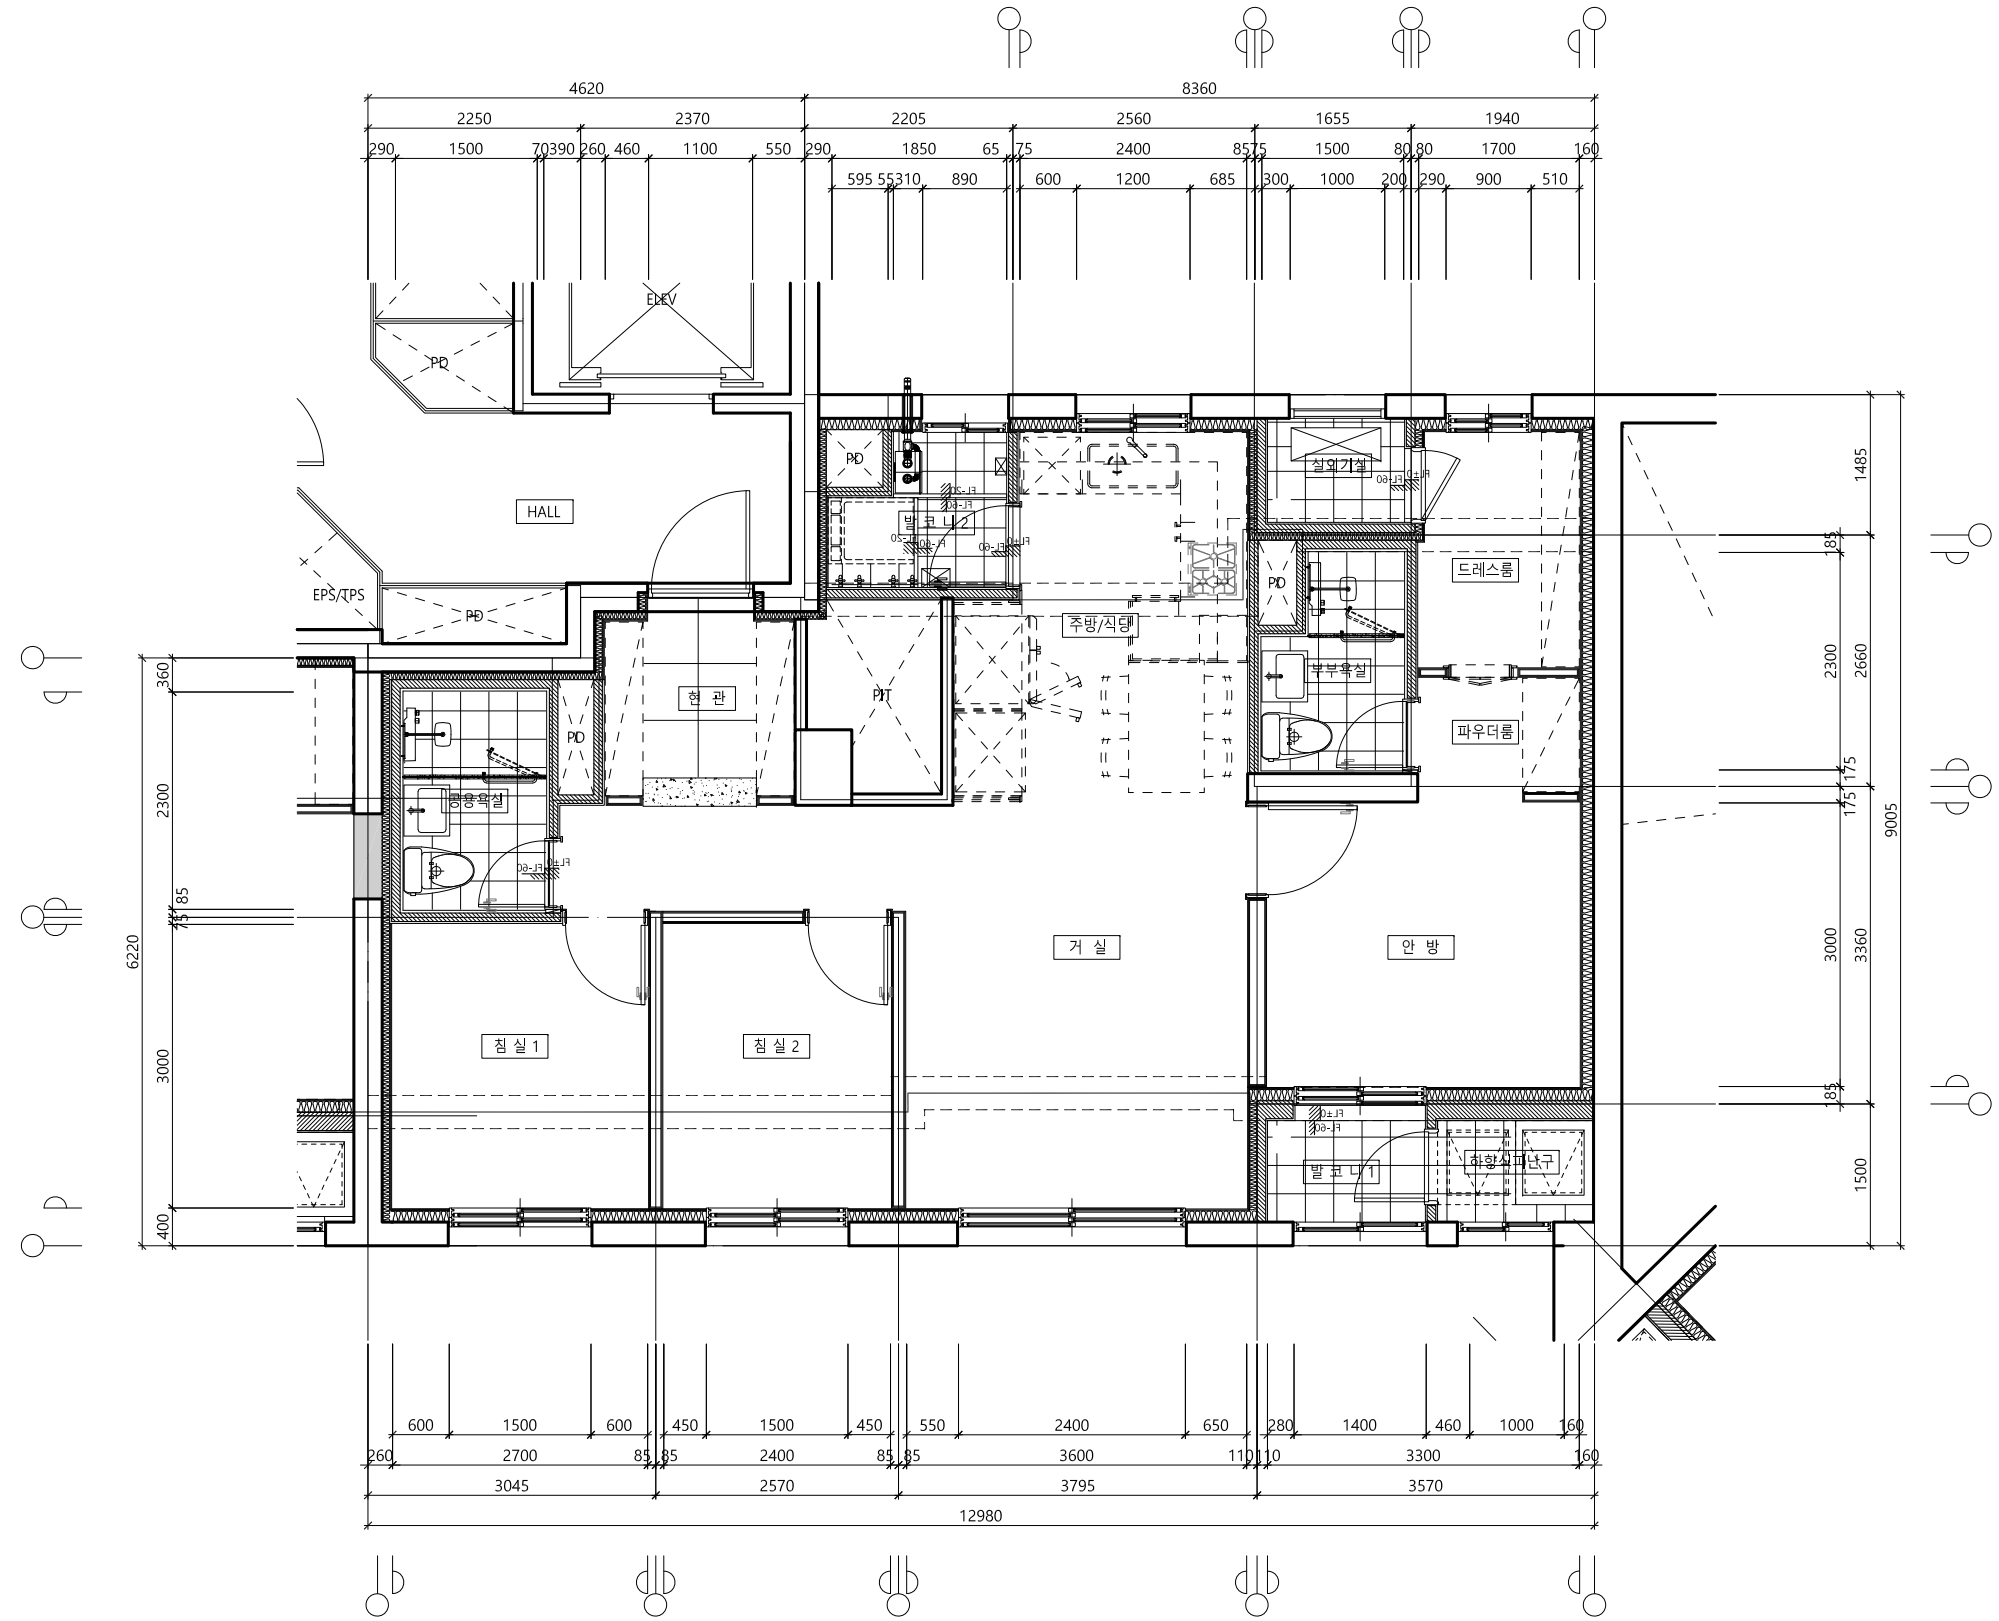

59Cm² 단위세대평면도(확장형)
SCALE : A1= 1 / 40
A3= 1 / 80

1					
0					
REV.	DATE	DESCRIPTION	BY	BY	APP.


SDglobal
TEL/82-02-6956-9300 SEOUL, KOREA
서울시 성동구 독성로1길 31(성수동1가) 서울솔 M타워 308호

DRAWING TITLE
59Cm² 단위세대평면도(확장형)

APPROVAL DATE 2025. 07.	APPROVED
PROJECT NO.	CHECKED 2
ENGINEER	CHECKED 1
SCALE A3: 1/ 80 A1: 1/ 40	DRAWN / DATE
DRAWING NO. A-000	REV.

과정3
가로주택정비사업

* NOTE.

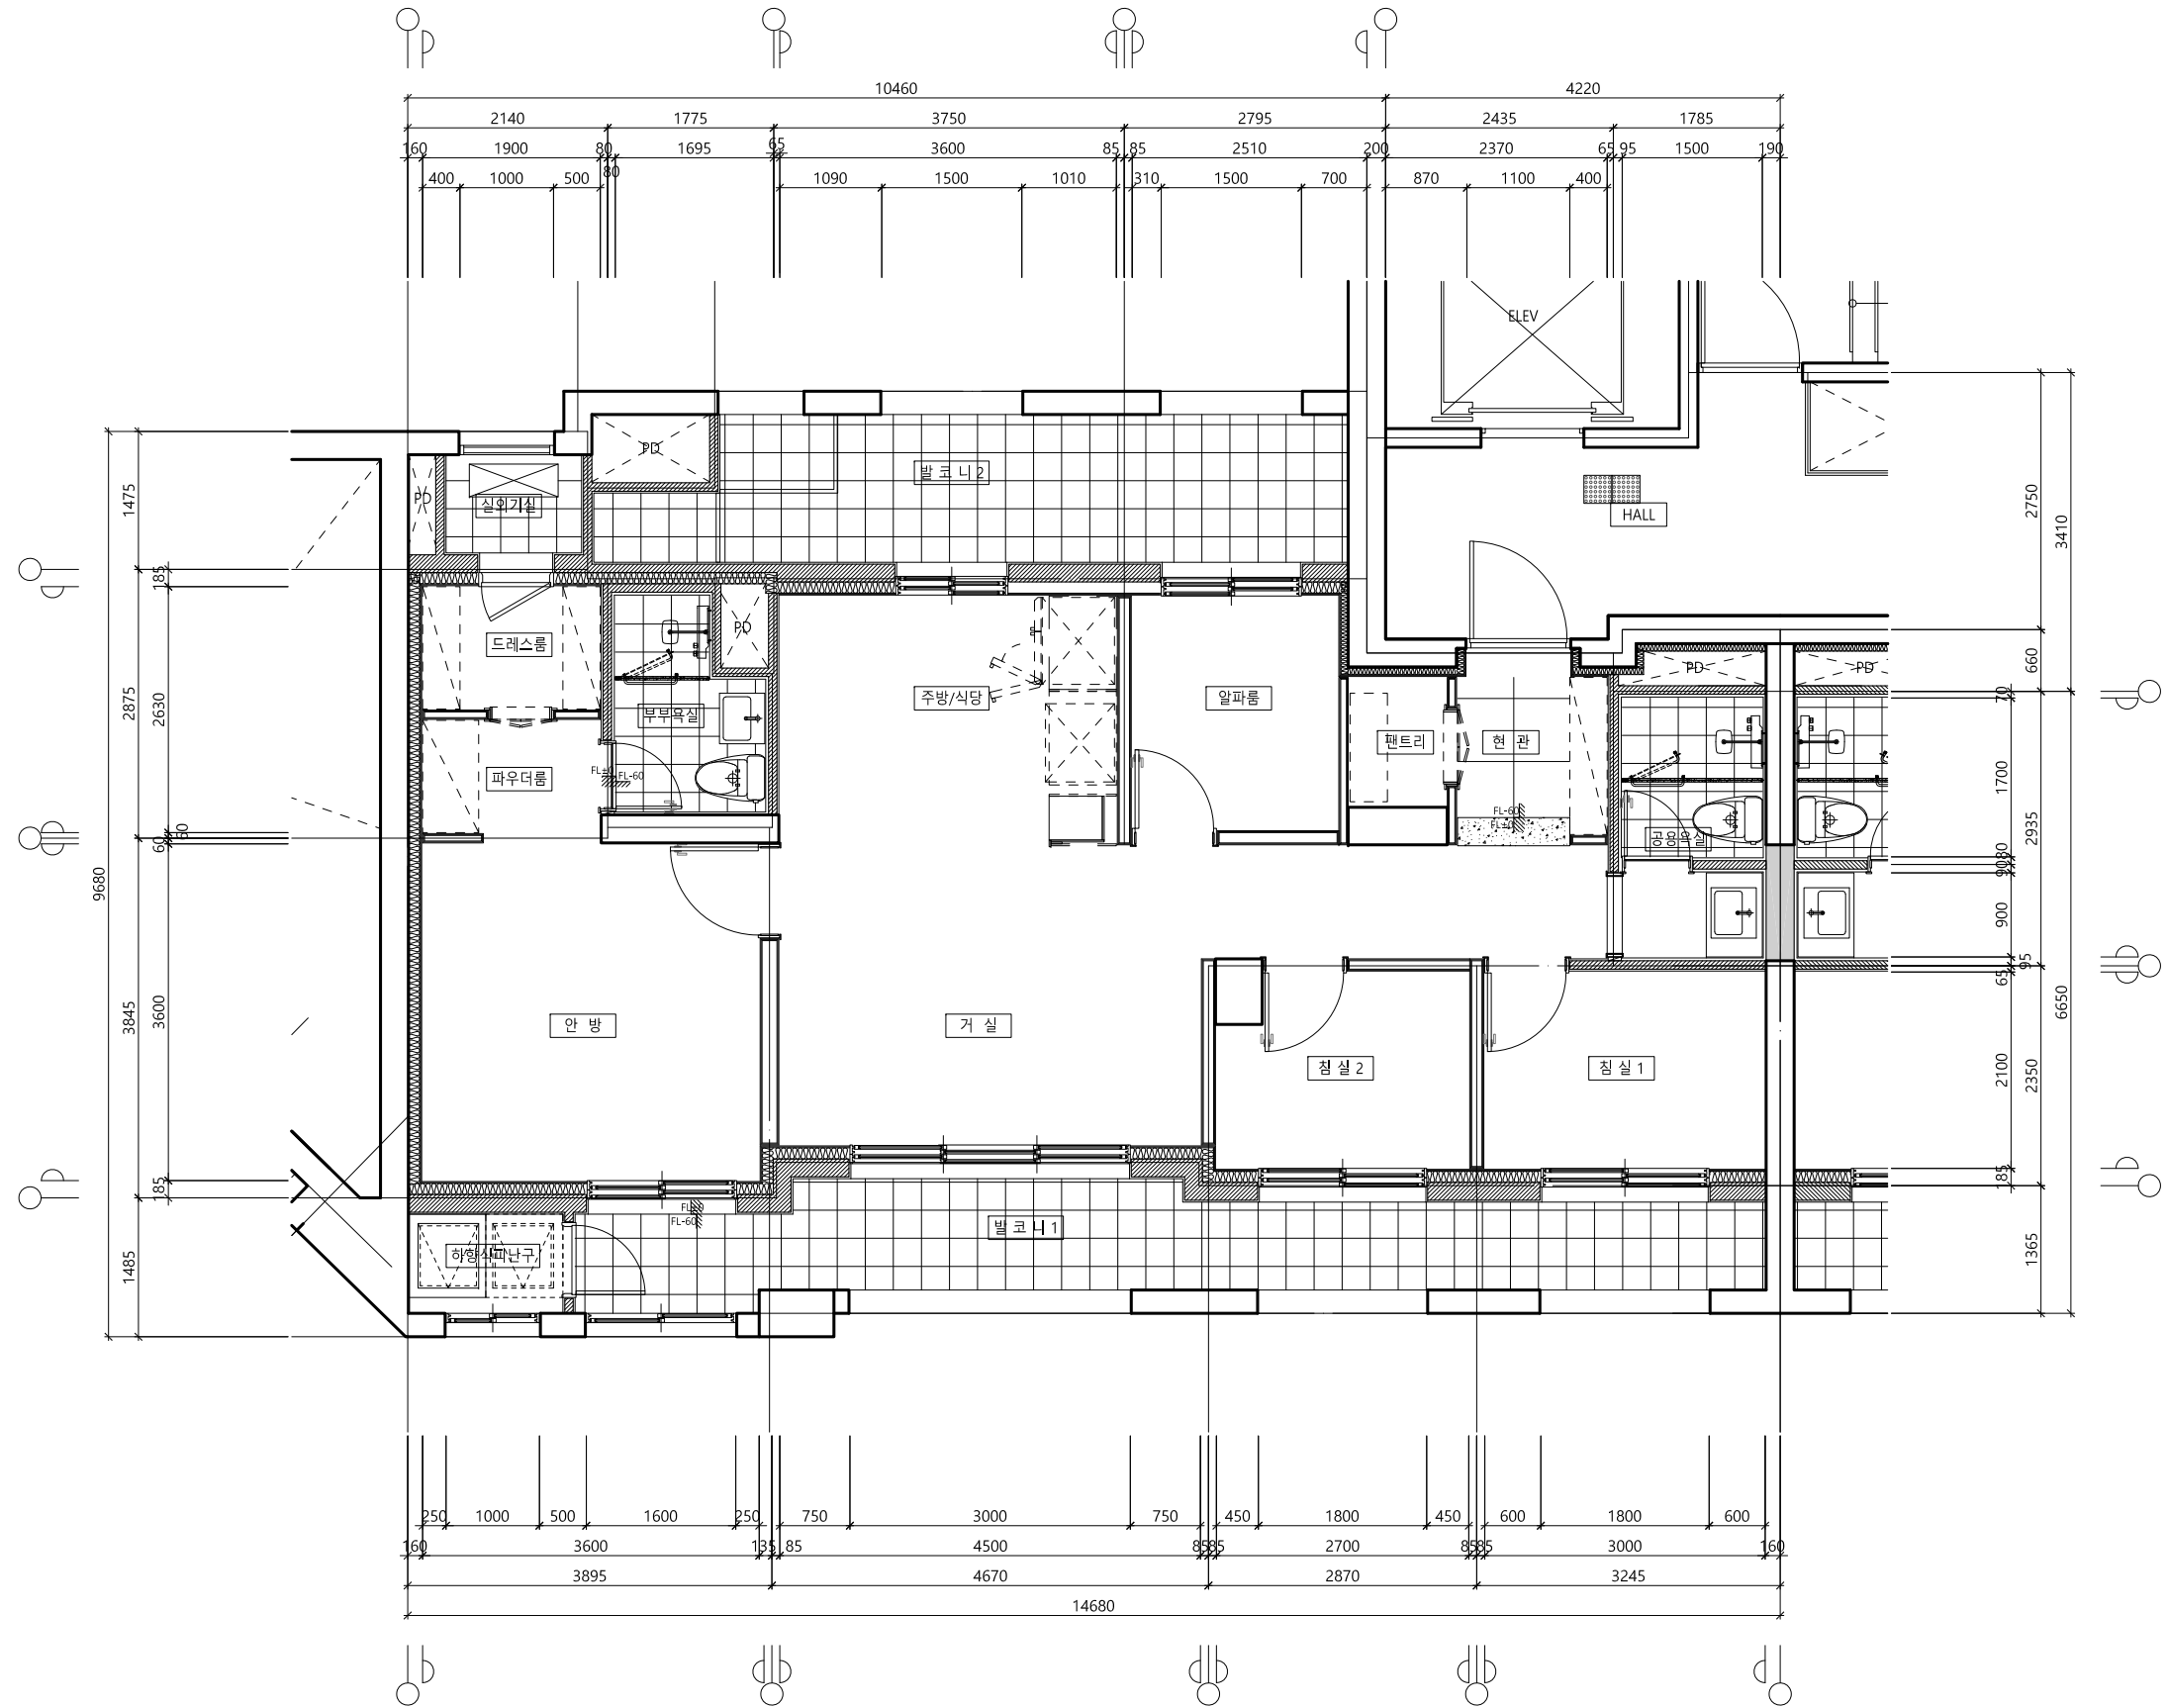

1
A

84m² 단위세대평면도(기본형)

SCALE : A1= 1 / 40
A3= 1 / 80

1					
0					
REV.	DATE	DESCRIPTION	BY	BY	APP.

SDglobal


I주SD글로벌건축사사무소
TEL/82-02-6956-9300 SEOUL, KOREA
서울시 성동구 독성로1길 31(성수동1가) 서울숲 M타워 308호

DRAWING TITLE
84m² 단위세대평면도(기본형)

APPROVAL DATE 2025. 07.	APPROVED
PROJECT NO.	CHECKED 2
ENGINEER	CHECKED 1
SCALE A3: 1/ 80	A1: 1/ 40
DRAWING NO. A-000	REV.

과정3
가로주택정비사업

* NOTE.

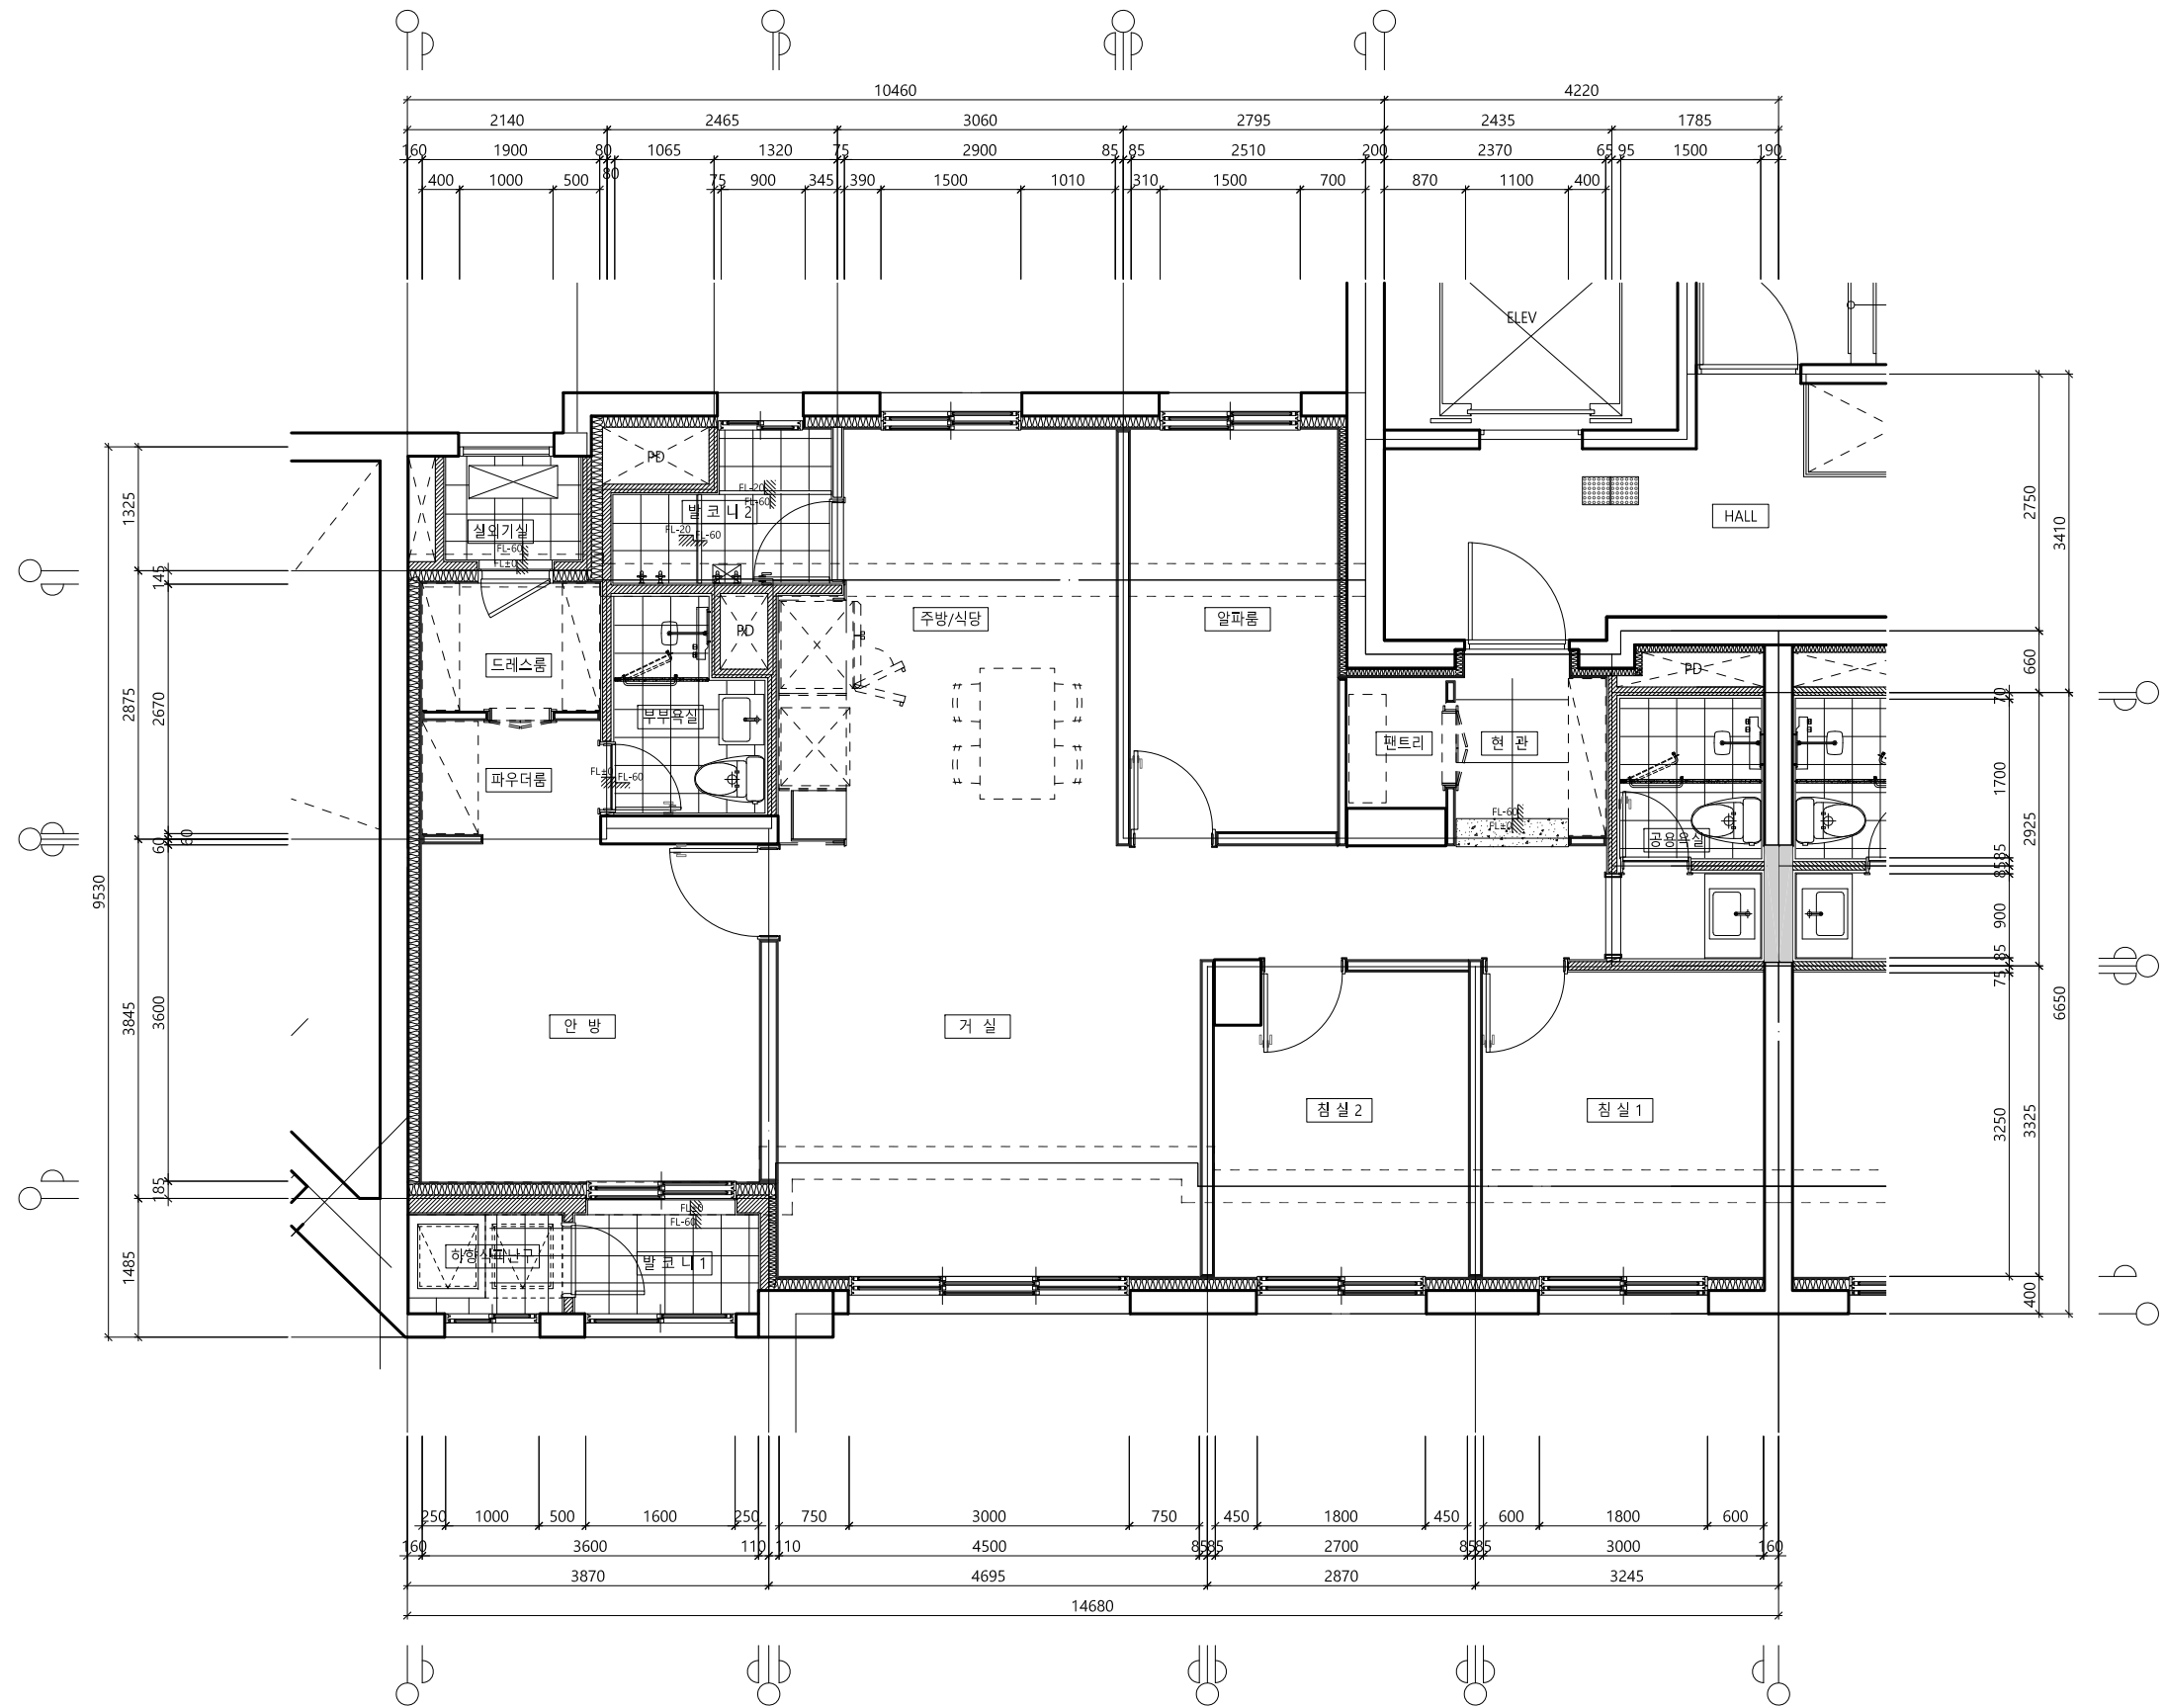

1
A

84m² 단위세대평면도(확장형)

SCALE : A1= 1 / 40
A3= 1 / 80

1					
0					
REV.	DATE	DESCRIPTION	BY	BY	APP.

SDglobal


I주ISD글로벌건축사사무소
TEL/82-02-6956-9300 SEOUL, KOREA
서울시 성동구 독성로1길 31(성수동1가) 서울숲 M타워 308호

DRAWING TITLE
84m² 단위세대평면도(확장형)

APPROVAL DATE 2025. 07.	APPROVED
PROJECT NO.	CHECKED 2
ENGINEER	CHECKED 1
SCALE A3: 1/ 80	A1: 1/ 40
DRAWING NO. A-000	REV.

과정3
가로주택정비사업

* NOTE.

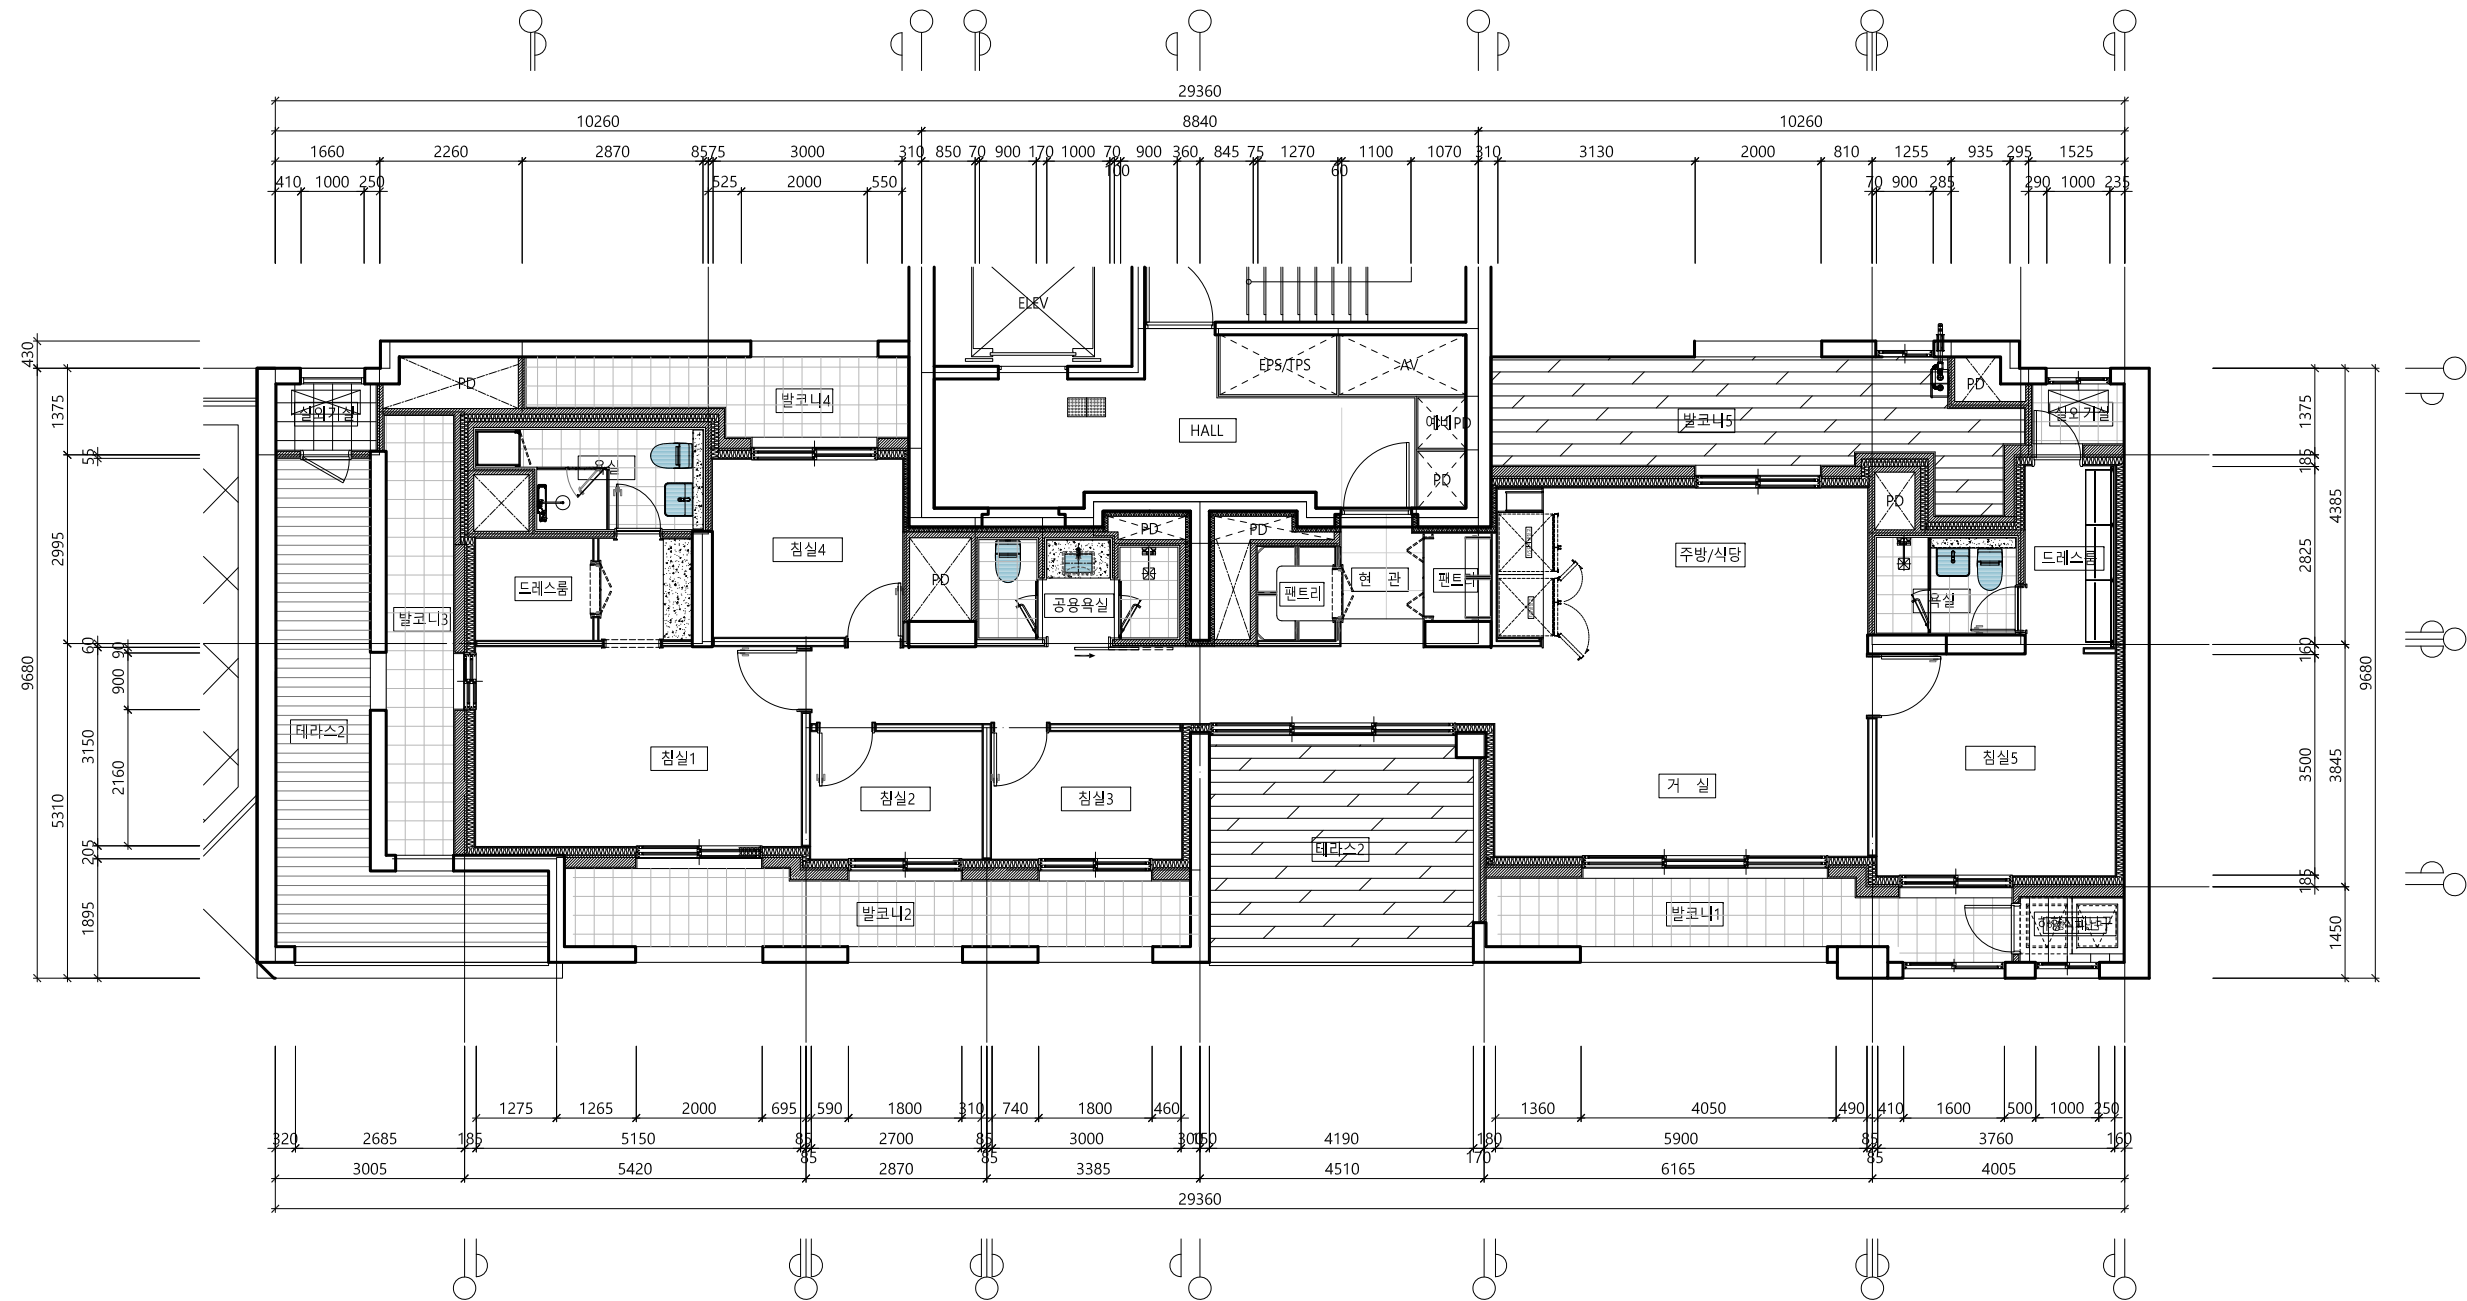

1 139m² 단위세대평면도(기본형)
SCALE : A1= 1 / 60
A3= 1 / 120

1					
0					
REV	DATE	DESCRIPTION	BY	BY	APP

SDglobal


TEL/82-02-6956-9300 SEOUL, KOREA
서울시 성동구 독성로1길 31(성수동1가) 서울을 M타워 308호

DRAWING TITLE
139m² 단위세대평면도(기본형)

APPROVAL DATE 2025. 07.	APPROVED
PROJECT NO.	CHECKED 2
ENGINEER	CHECKED 1
SCALE A3: 1/ 120 A1: 1/ 60	DRAWN / DATE
DRAWING NO. A-000	REV.

과정3
가로주택정비사업

* NOTE.

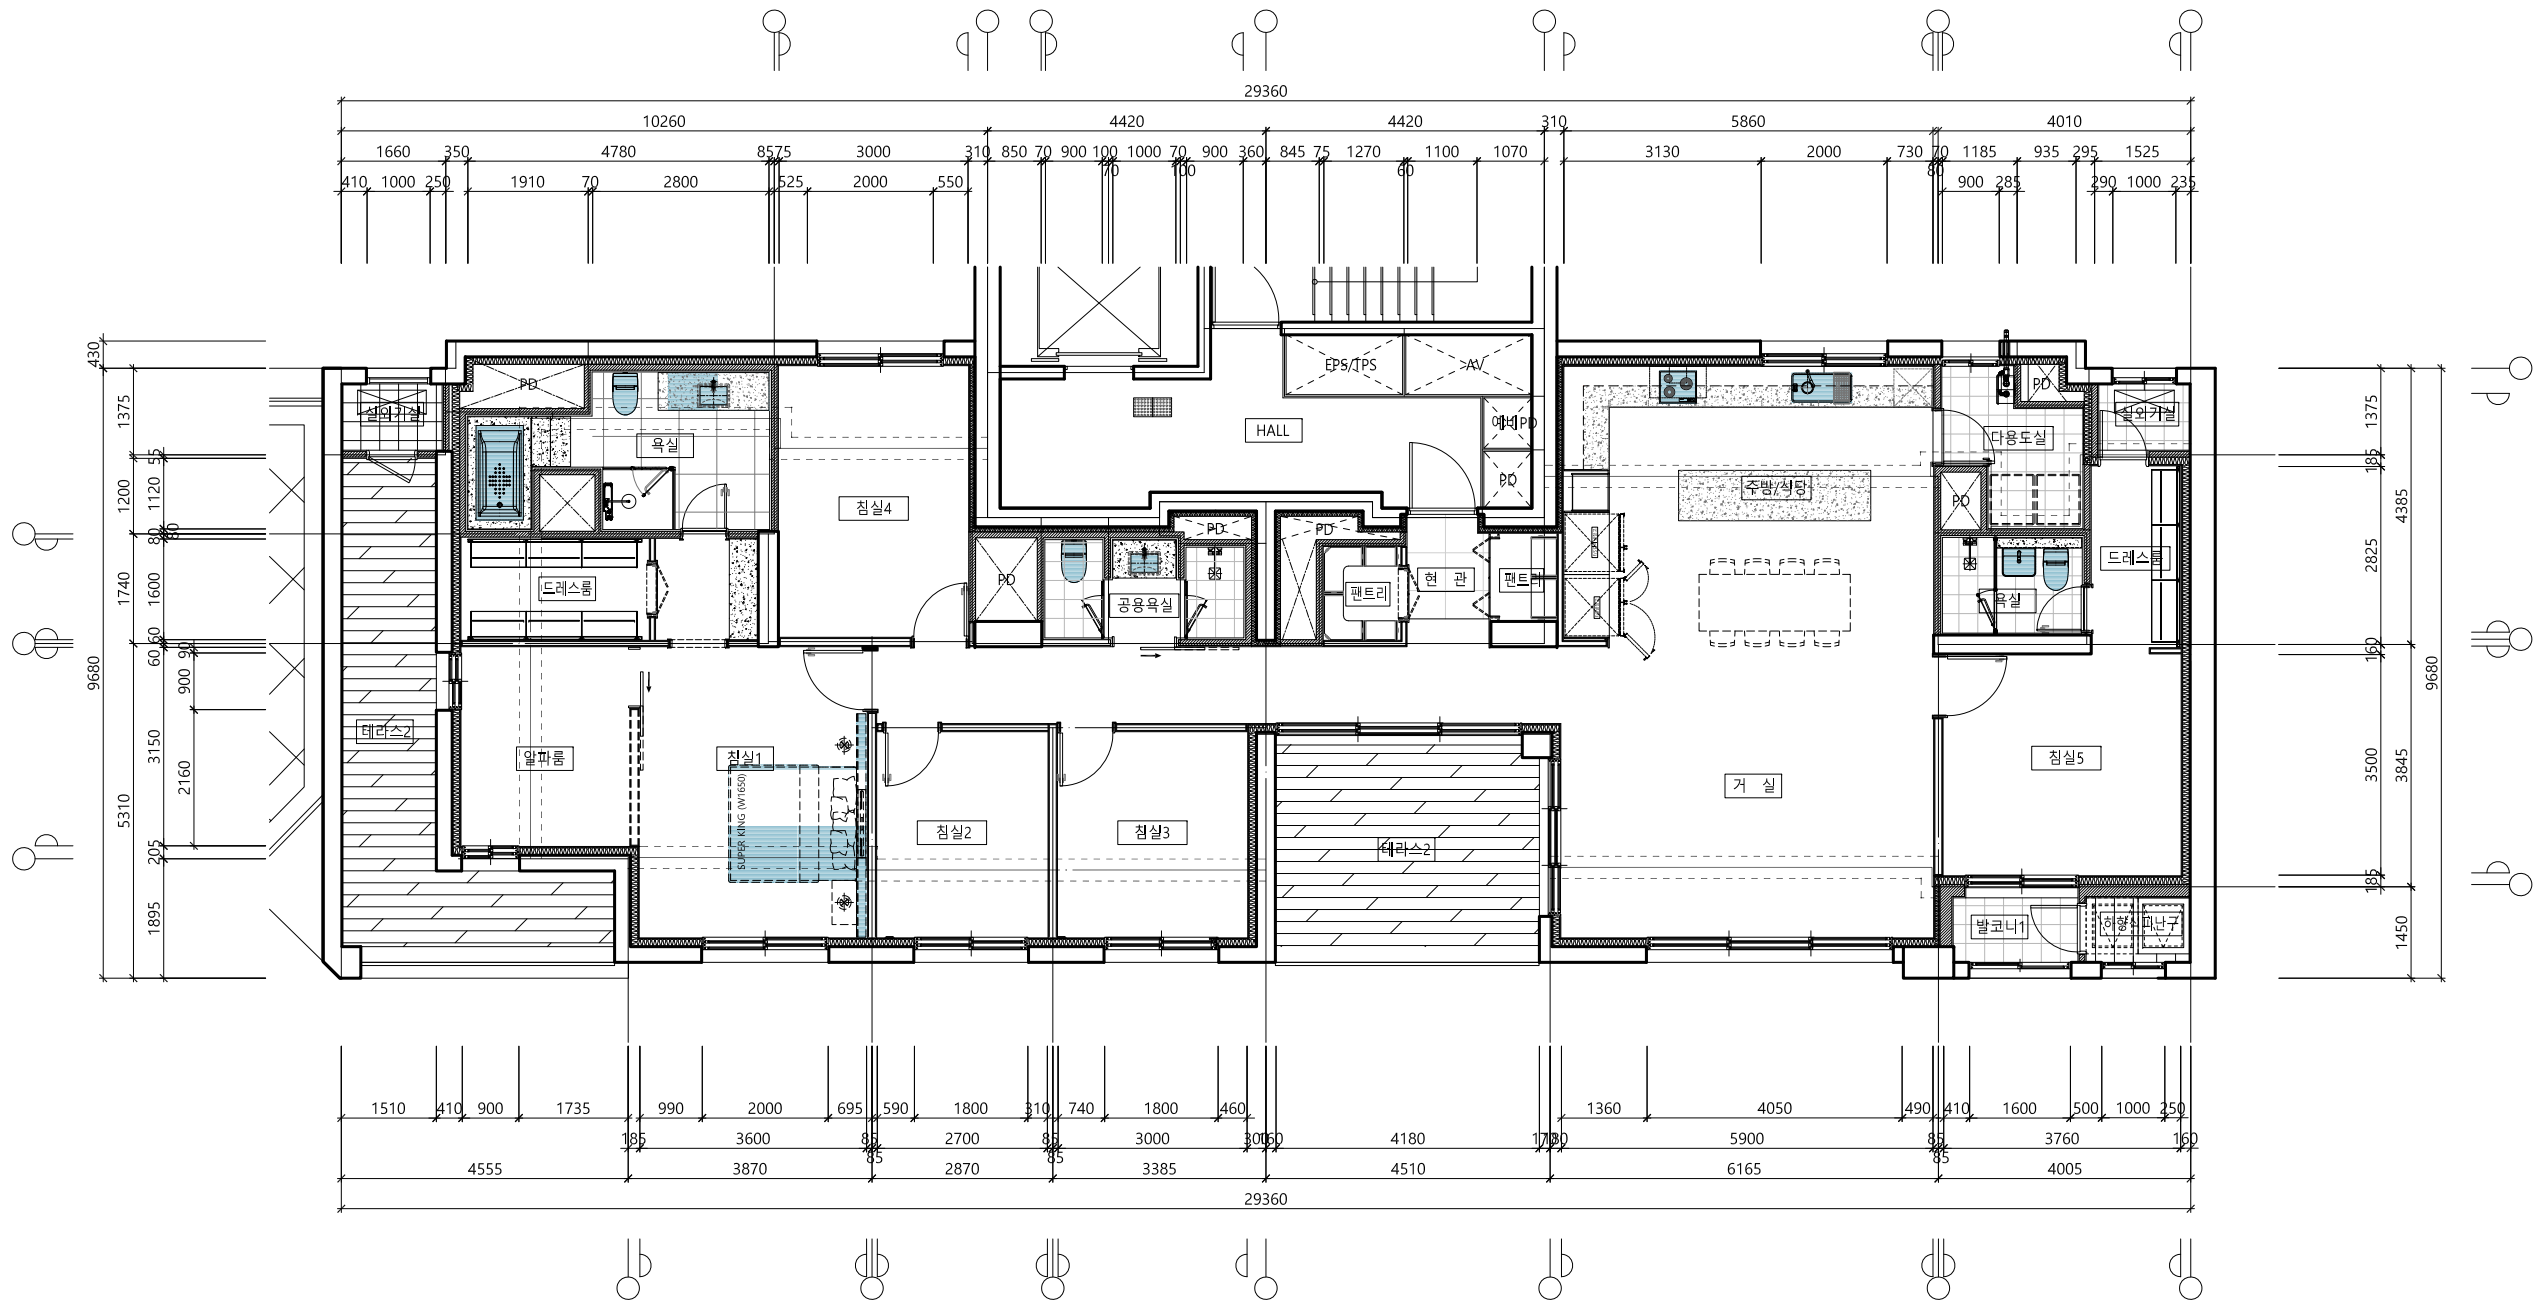

1
A 139m² 단위세대평면도(확장형)
SCALE : A1= 1 / 60
A3= 1 / 120

REV.	DATE	DESCRIPTION	BY	BY	APP.
1					
0					

SDglobal


TEL/82-02-6956-9300 SEOUL, KOREA
서울시 성동구 독성로1길 31(성수동1가) 서울을 M타워 308호

DRAWING TITLE
139m² 단위세대평면도(확장형)

APPROVAL DATE 2025. 07.	APPROVED
PROJECT NO.	CHECKED 2
ENGINEER	CHECKED 1
SCALE A3: 1/ 120 A1: 1/ 60	DRAWN / DATE
DRAWING NO. A-000	REV.

동평면도

* NOTE.

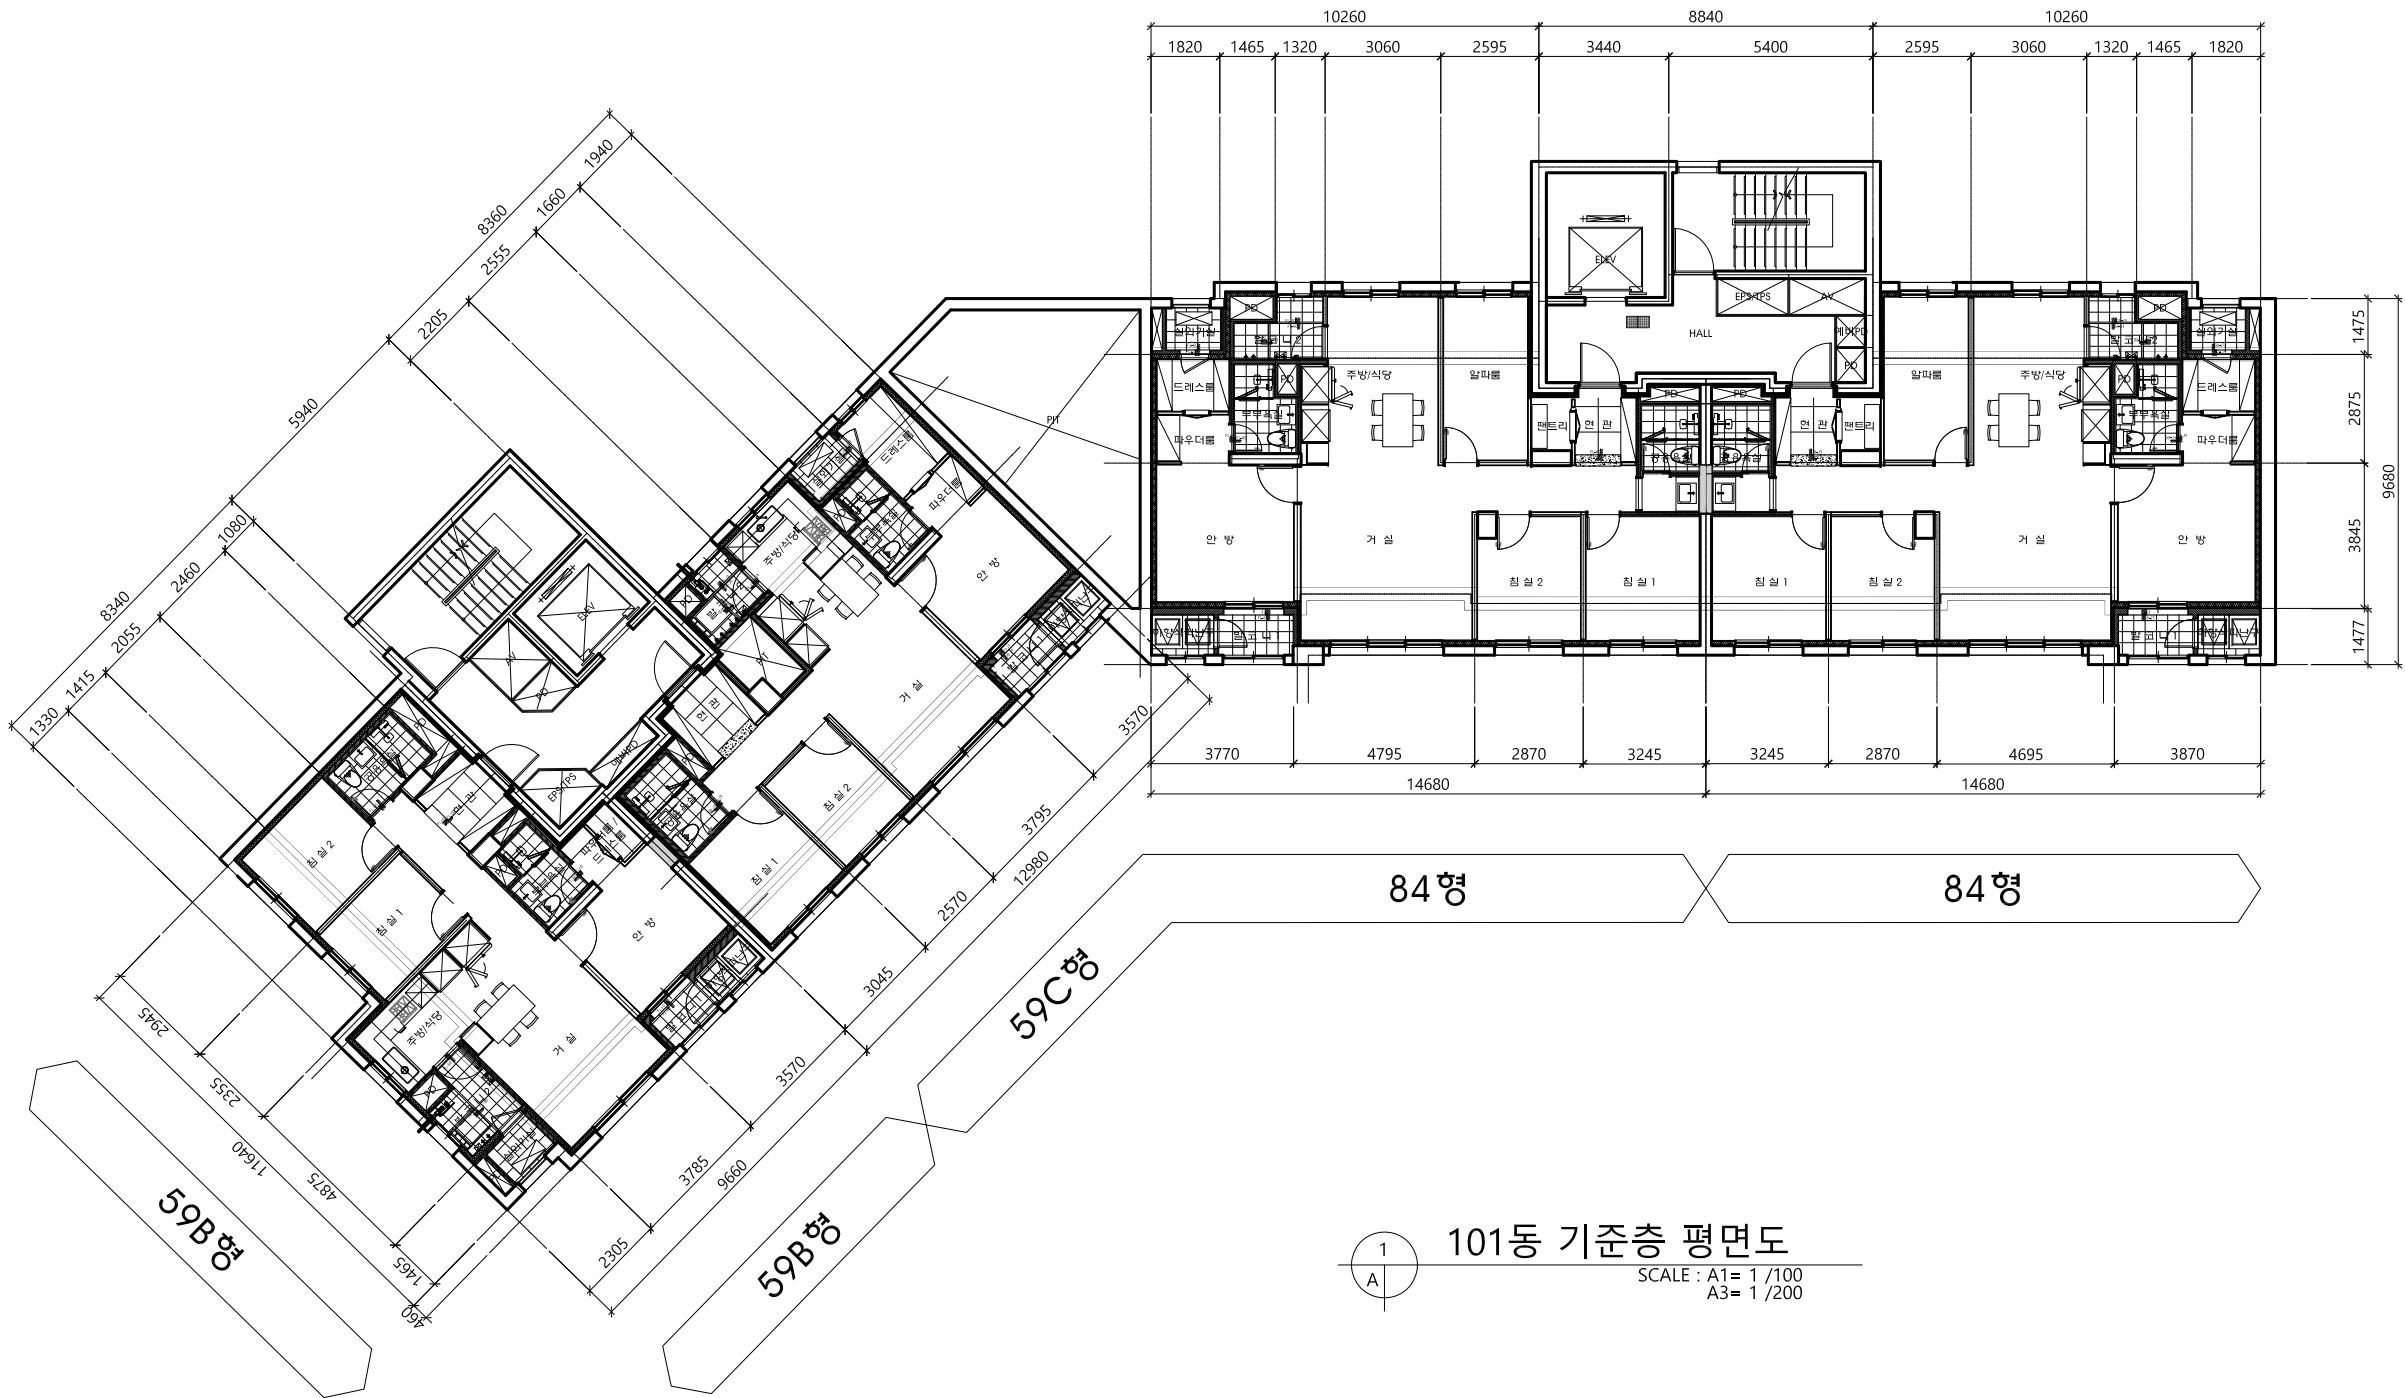

101동 기준층 평면도
SCALE : A1= 1 /100
A3= 1 /200

1					
0					
REV.	DATE	DESCRIPTION	BY	BY	APP.


SDglobal

TEL/82-02-6956-9300 SEOUL, KOREA
서울시 성동구 독성로1길 31(성수동1가) 서울솔 M타워 308호

DRAWING TITLE	
101동 기준층 평면도	
APPROVAL DATE	APPROVED
2025. 07.	
PROJECT NO.	CHECKED 2
ENGINEER	CHECKED 1
SCALE	DRAWN / DATE
A3: 1/ 200 A1: 1/ 100	
DRAWING NO.	REV.

과정3
가로주택정비사업

* NOTE.

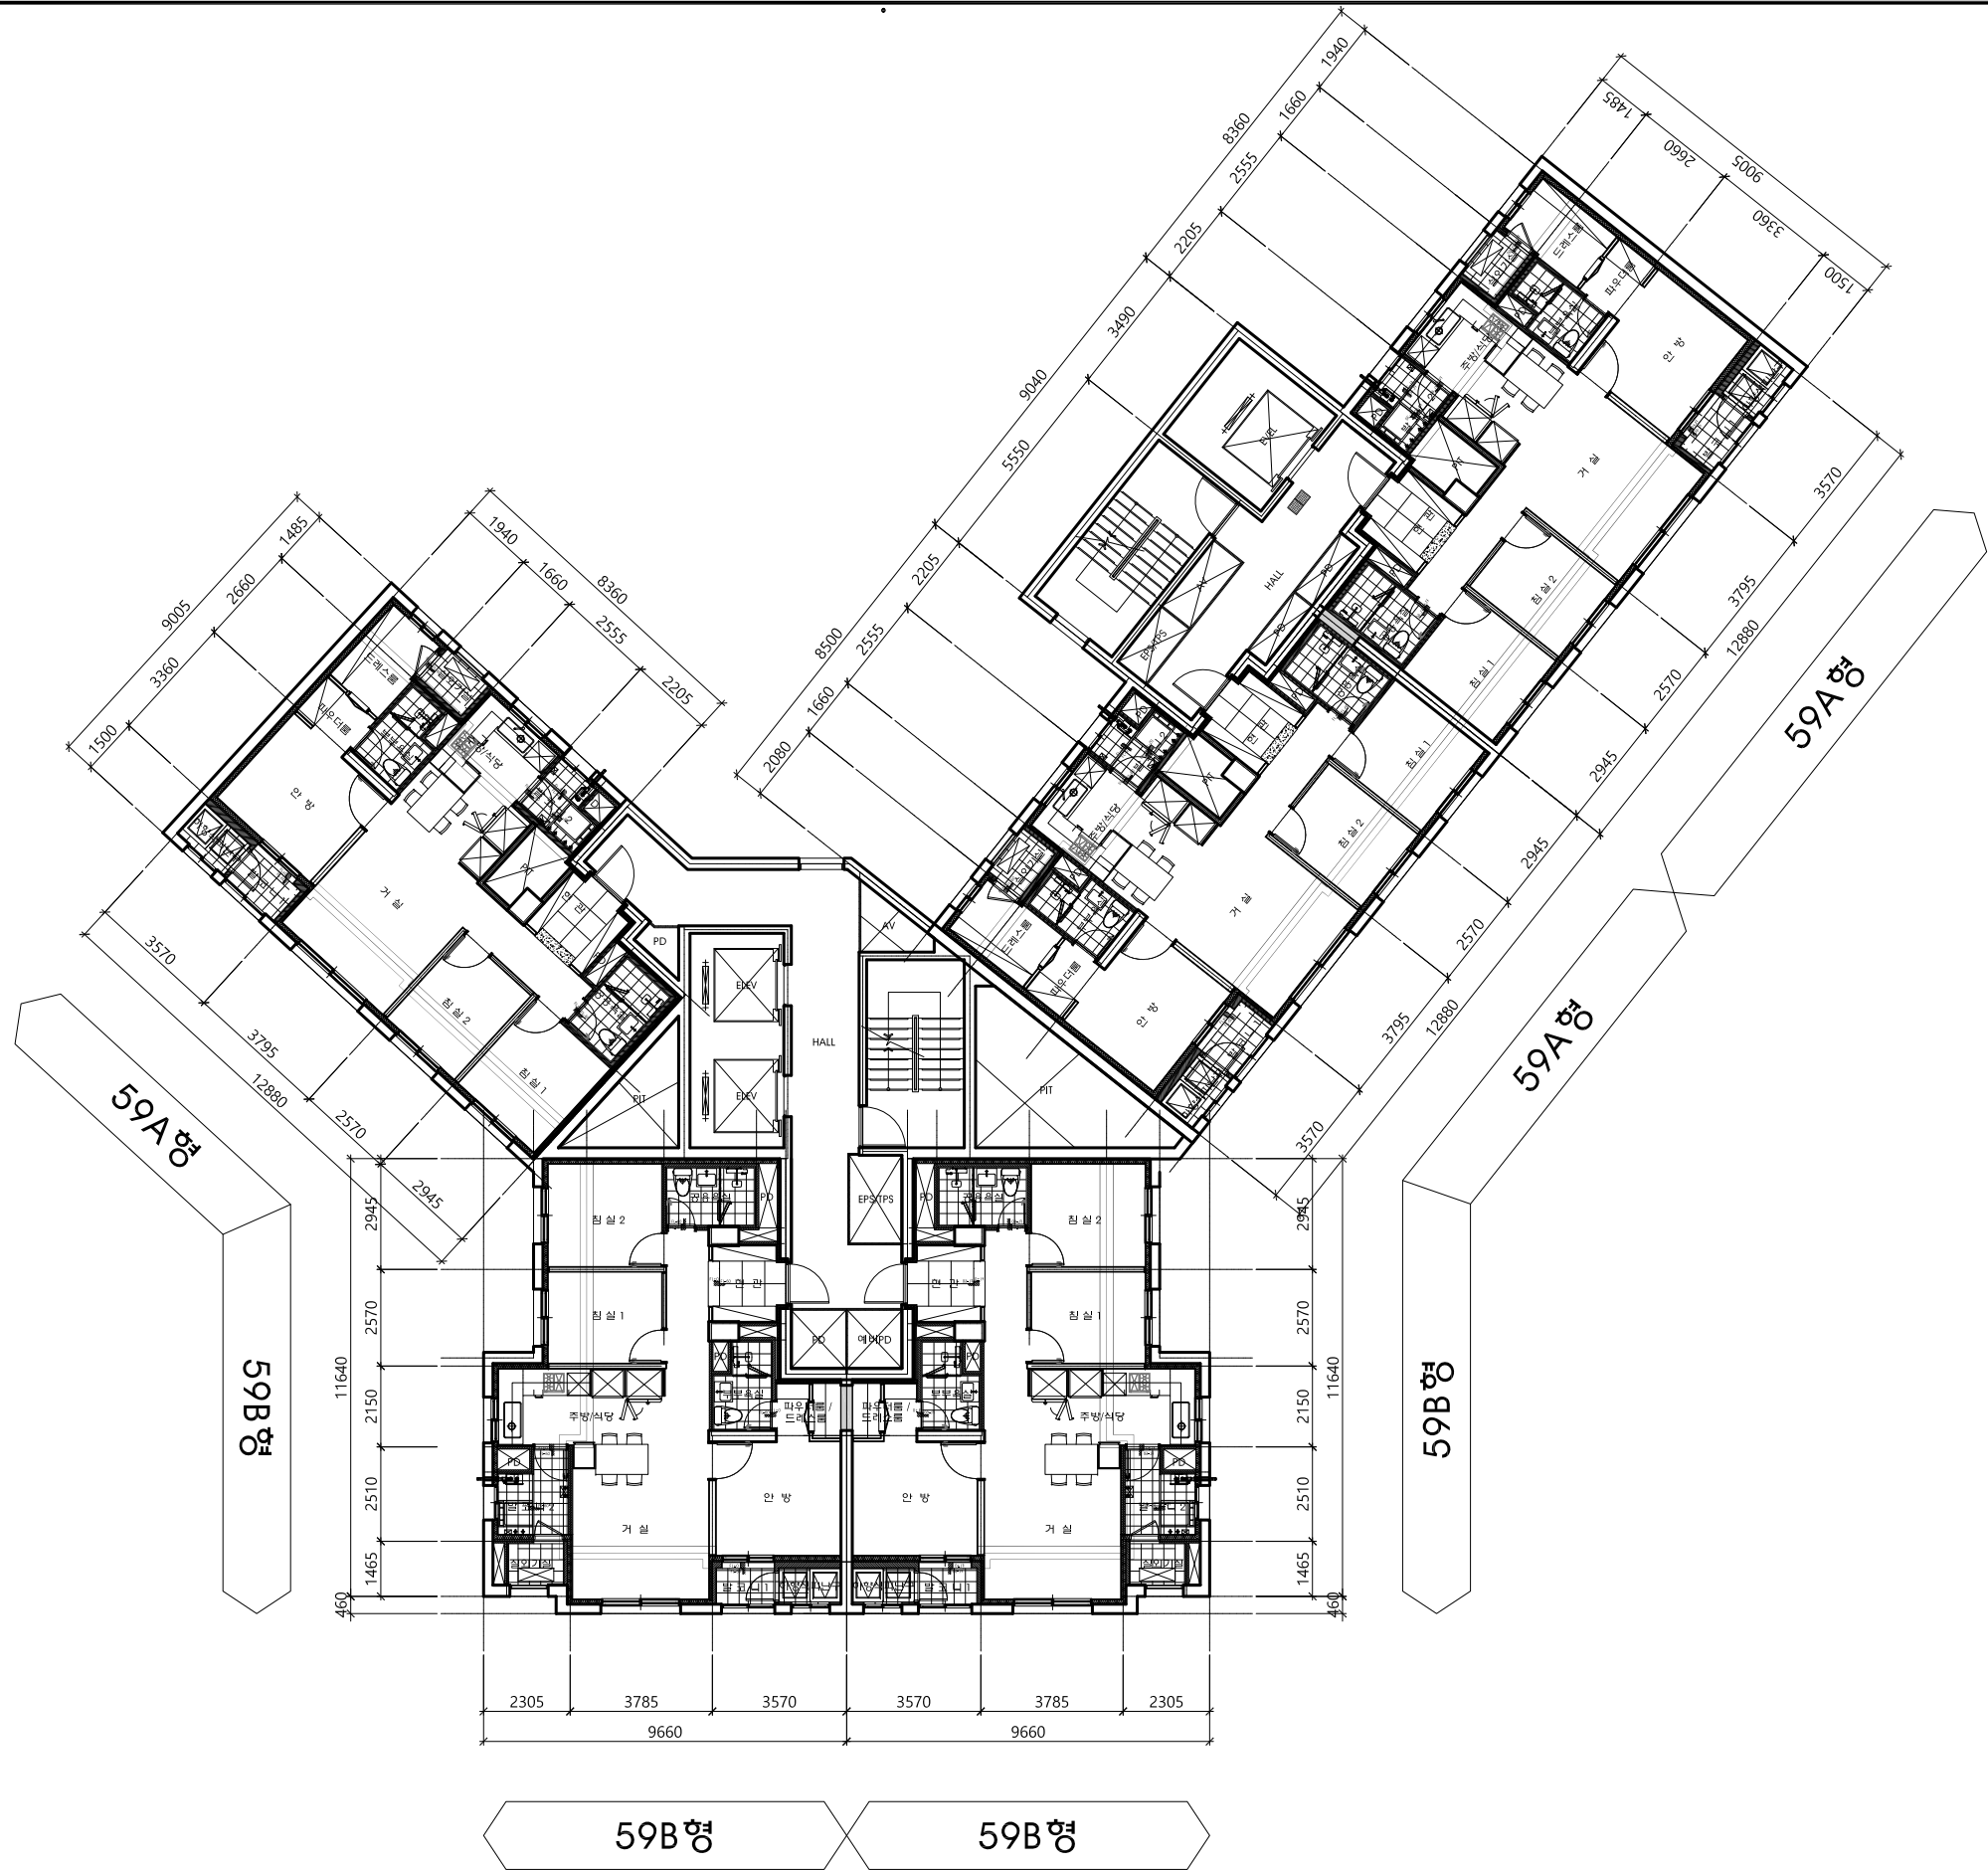

102동 기준층 평면도
SCALE : A1= 1 /100
A3= 1 /200

1					
0					
REV.	DATE	DESCRIPTION	BY	BY	APP.


SDglobal

TEL/82-02-6956-9300 SEOUL, KOREA
서울시 성동구 독성로1길 31(성수동1가) 서울솔 M타워 308호

DRAWING TITLE
102동 기준층 평면도

APPROVAL DATE 2025. 07.	APPROVED
PROJECT NO.	CHECKED 2
ENGINEER	CHECKED 1
SCALE A3: 1/ 200 A1: 1/ 100	DRAWN / DATE
DRAWING NO.	REV.

* NOTE.

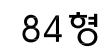

SCALE : A1= 1 /100
A3= 1 /200

SCALE	DRAWN / DATE	
A3: 1/ 200	A1: 1/ 100	
DRAWING NO.		REV.

지하주차장평면도

* NOTE.

1					
0					
REV.	DATE	DESCRIPTION	BY	BY	APP

TEL/82-02-6956-9300 SEOUL, KOREA
서울시 성동구 독성로1길 31(성수동1가) 서울숲 M타워 308호

지하4층 평면도

APPROVAL DATE 2025. 07.		APPROVED	
PROJECT NO.		CHECKED 2	
ENGINEER		CHECKED 1	
SCALE A3: 1/ 600	A1: 1/ 300	DRAWN / DATE	
DRAWING NO. A-000			REV.

* NOTE.

1					
0					
REV.	DATE	DESCRIPTION	BY	BY	APP


TEL/82-02-6956-9300 SEOUL, KOREA
서울시 성동구 독성로1길 31(성수동1가) 서울숲 M타워 308호

지하3층 평면도

APPROVAL DATE 2025. 07.		APPROVED	
PROJECT NO.		CHECKED 2	
ENGINEER		CHECKED 1	
SCALE A3: 1/600	A1: 1/300	DRAWN / DATE	
DRAWING NO. A-000			REV.

과정3
가로주택정비사업

* NOTE.

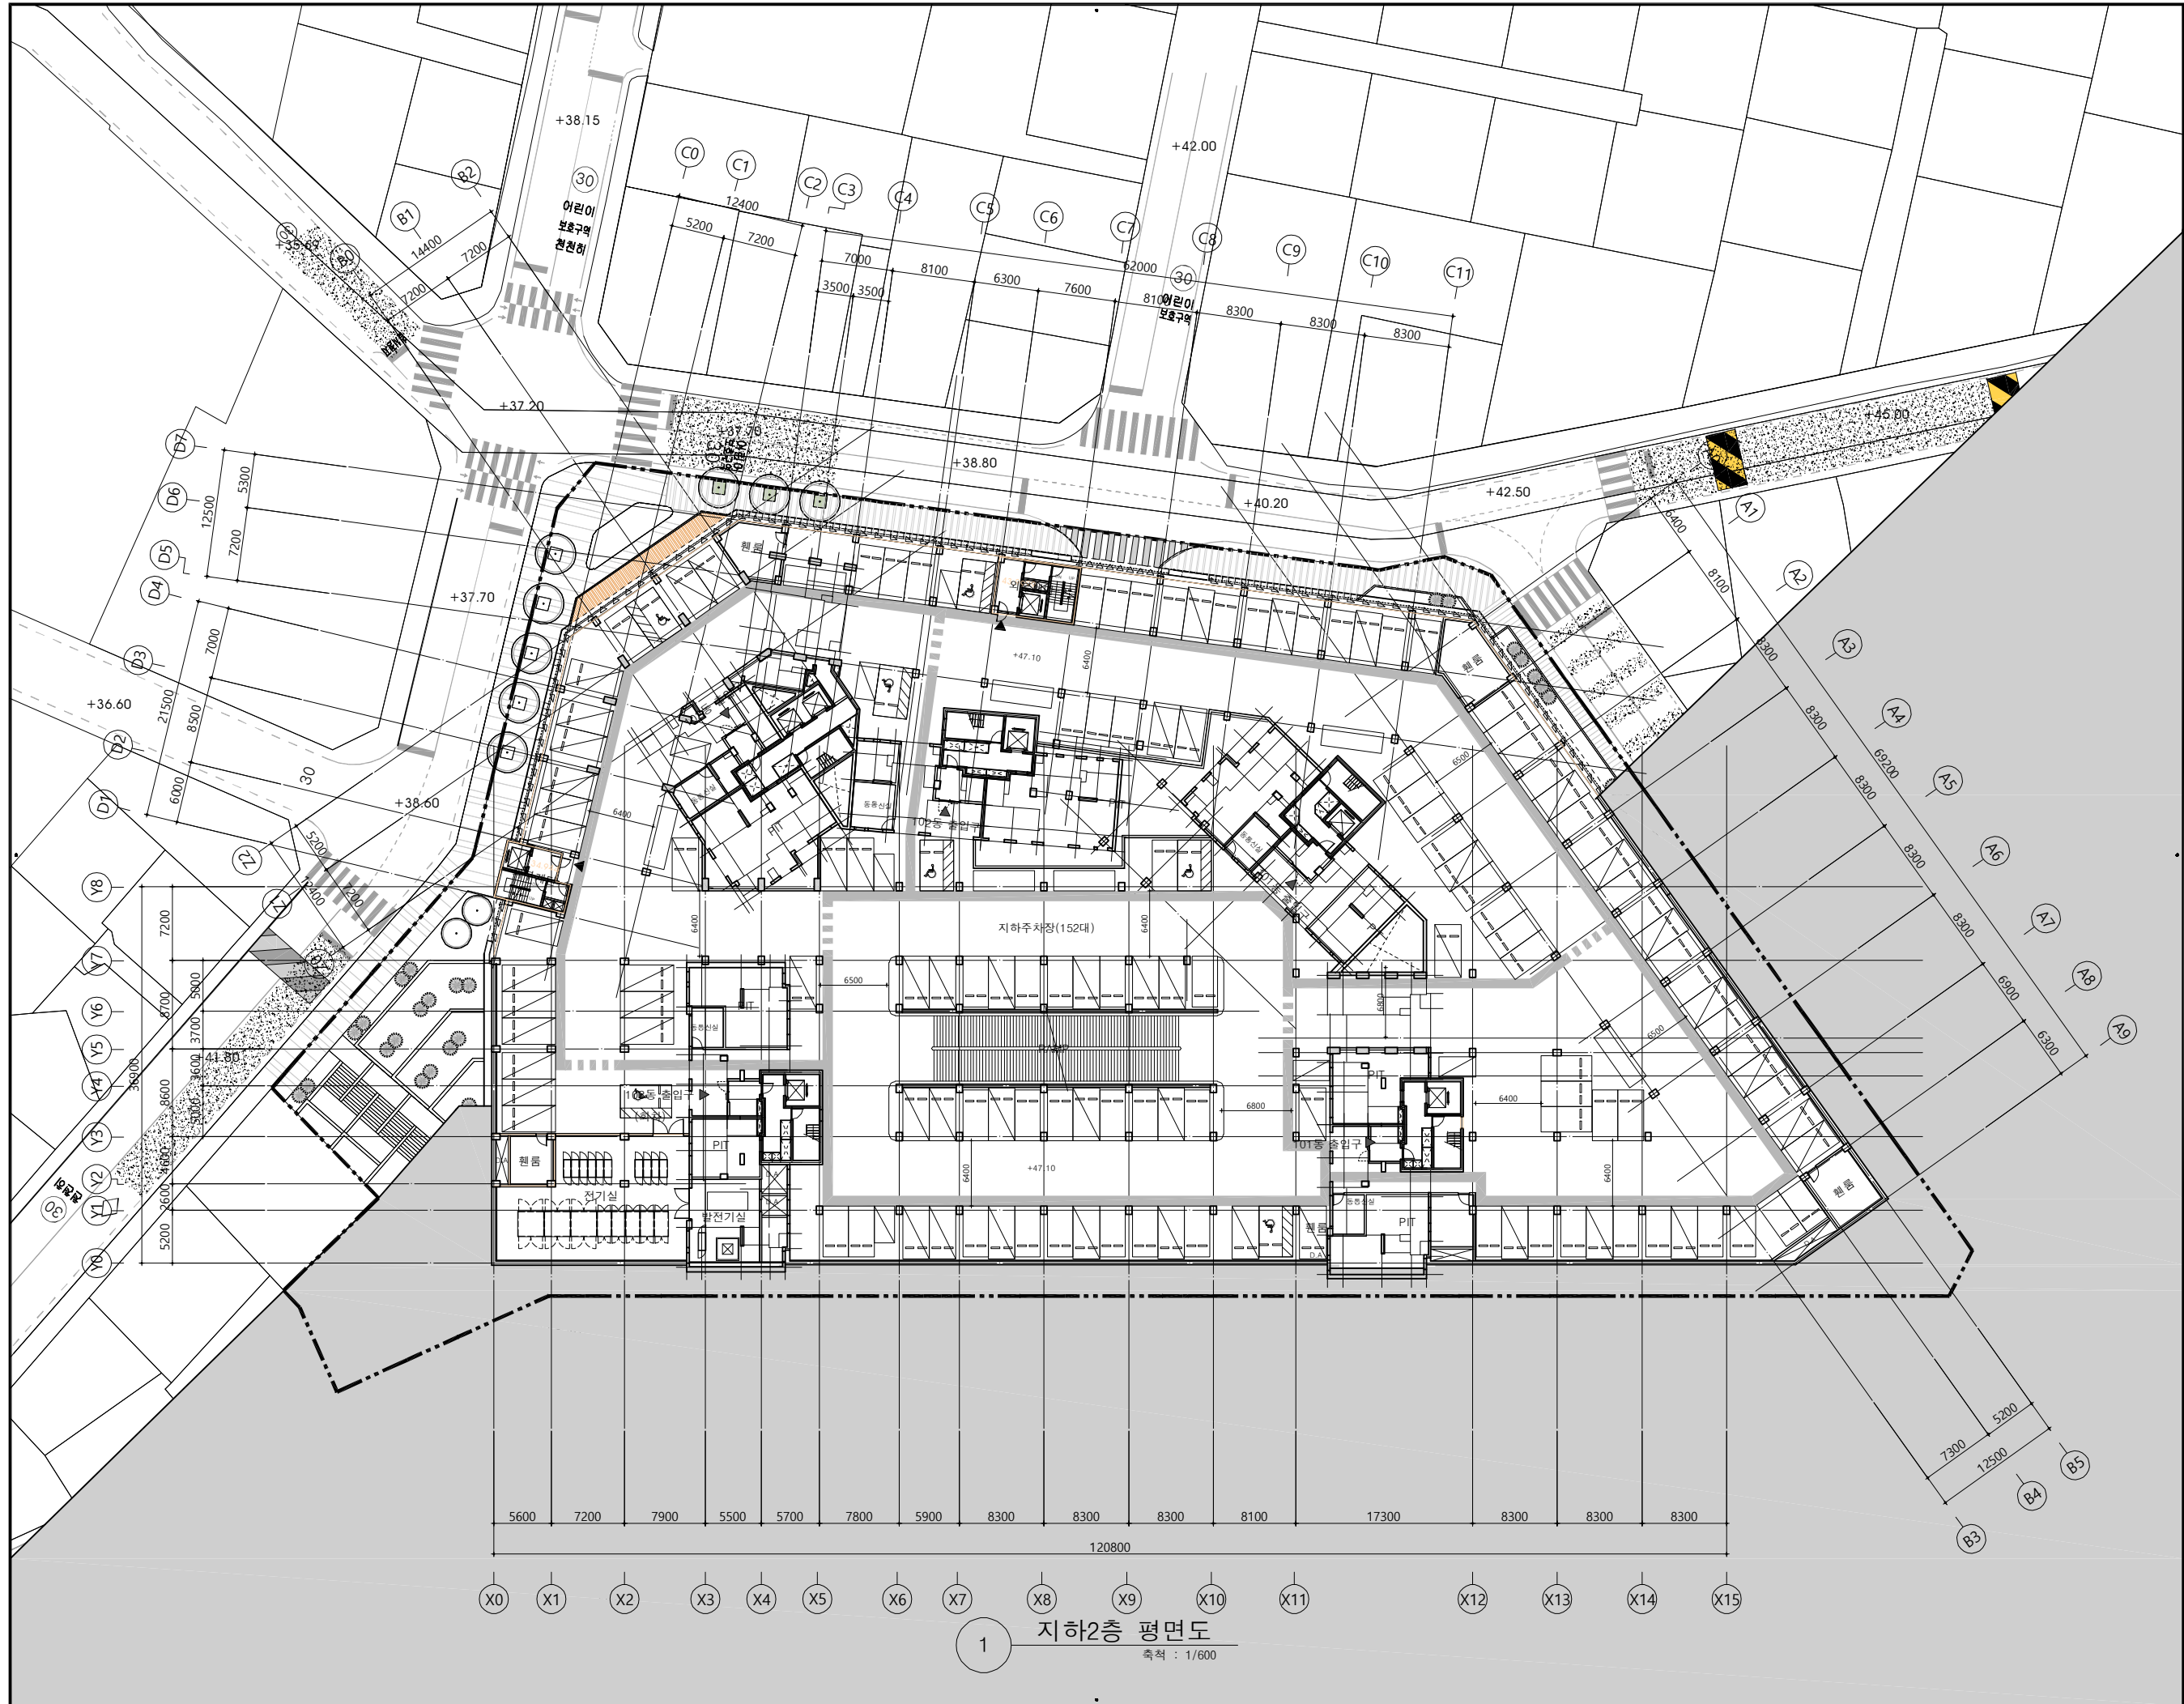

지하2층 평면도

축척 : 1/600

1					
0					
REV.	DATE	DESCRIPTION	BY	BY	APP.

SDglobal

TEL/82-02-6956-9300 SEOUL, KOREA
서울시 성동구 복성로1길 31(성수동1가) 서울을 M타워 308호


DRAWING TITLE

지하2층 평면도

APPROVAL DATE	APPROVED
2025. 07.	
PROJECT NO.	CHECKED 2
ENGINEER	CHECKED 1
SCALE	DRAWN / DATE
A3: 1/ 600 A1: 1/ 300	
DRAWING NO.	REV.
A-000	

과정3
가로주택정비사업

* NOTE.

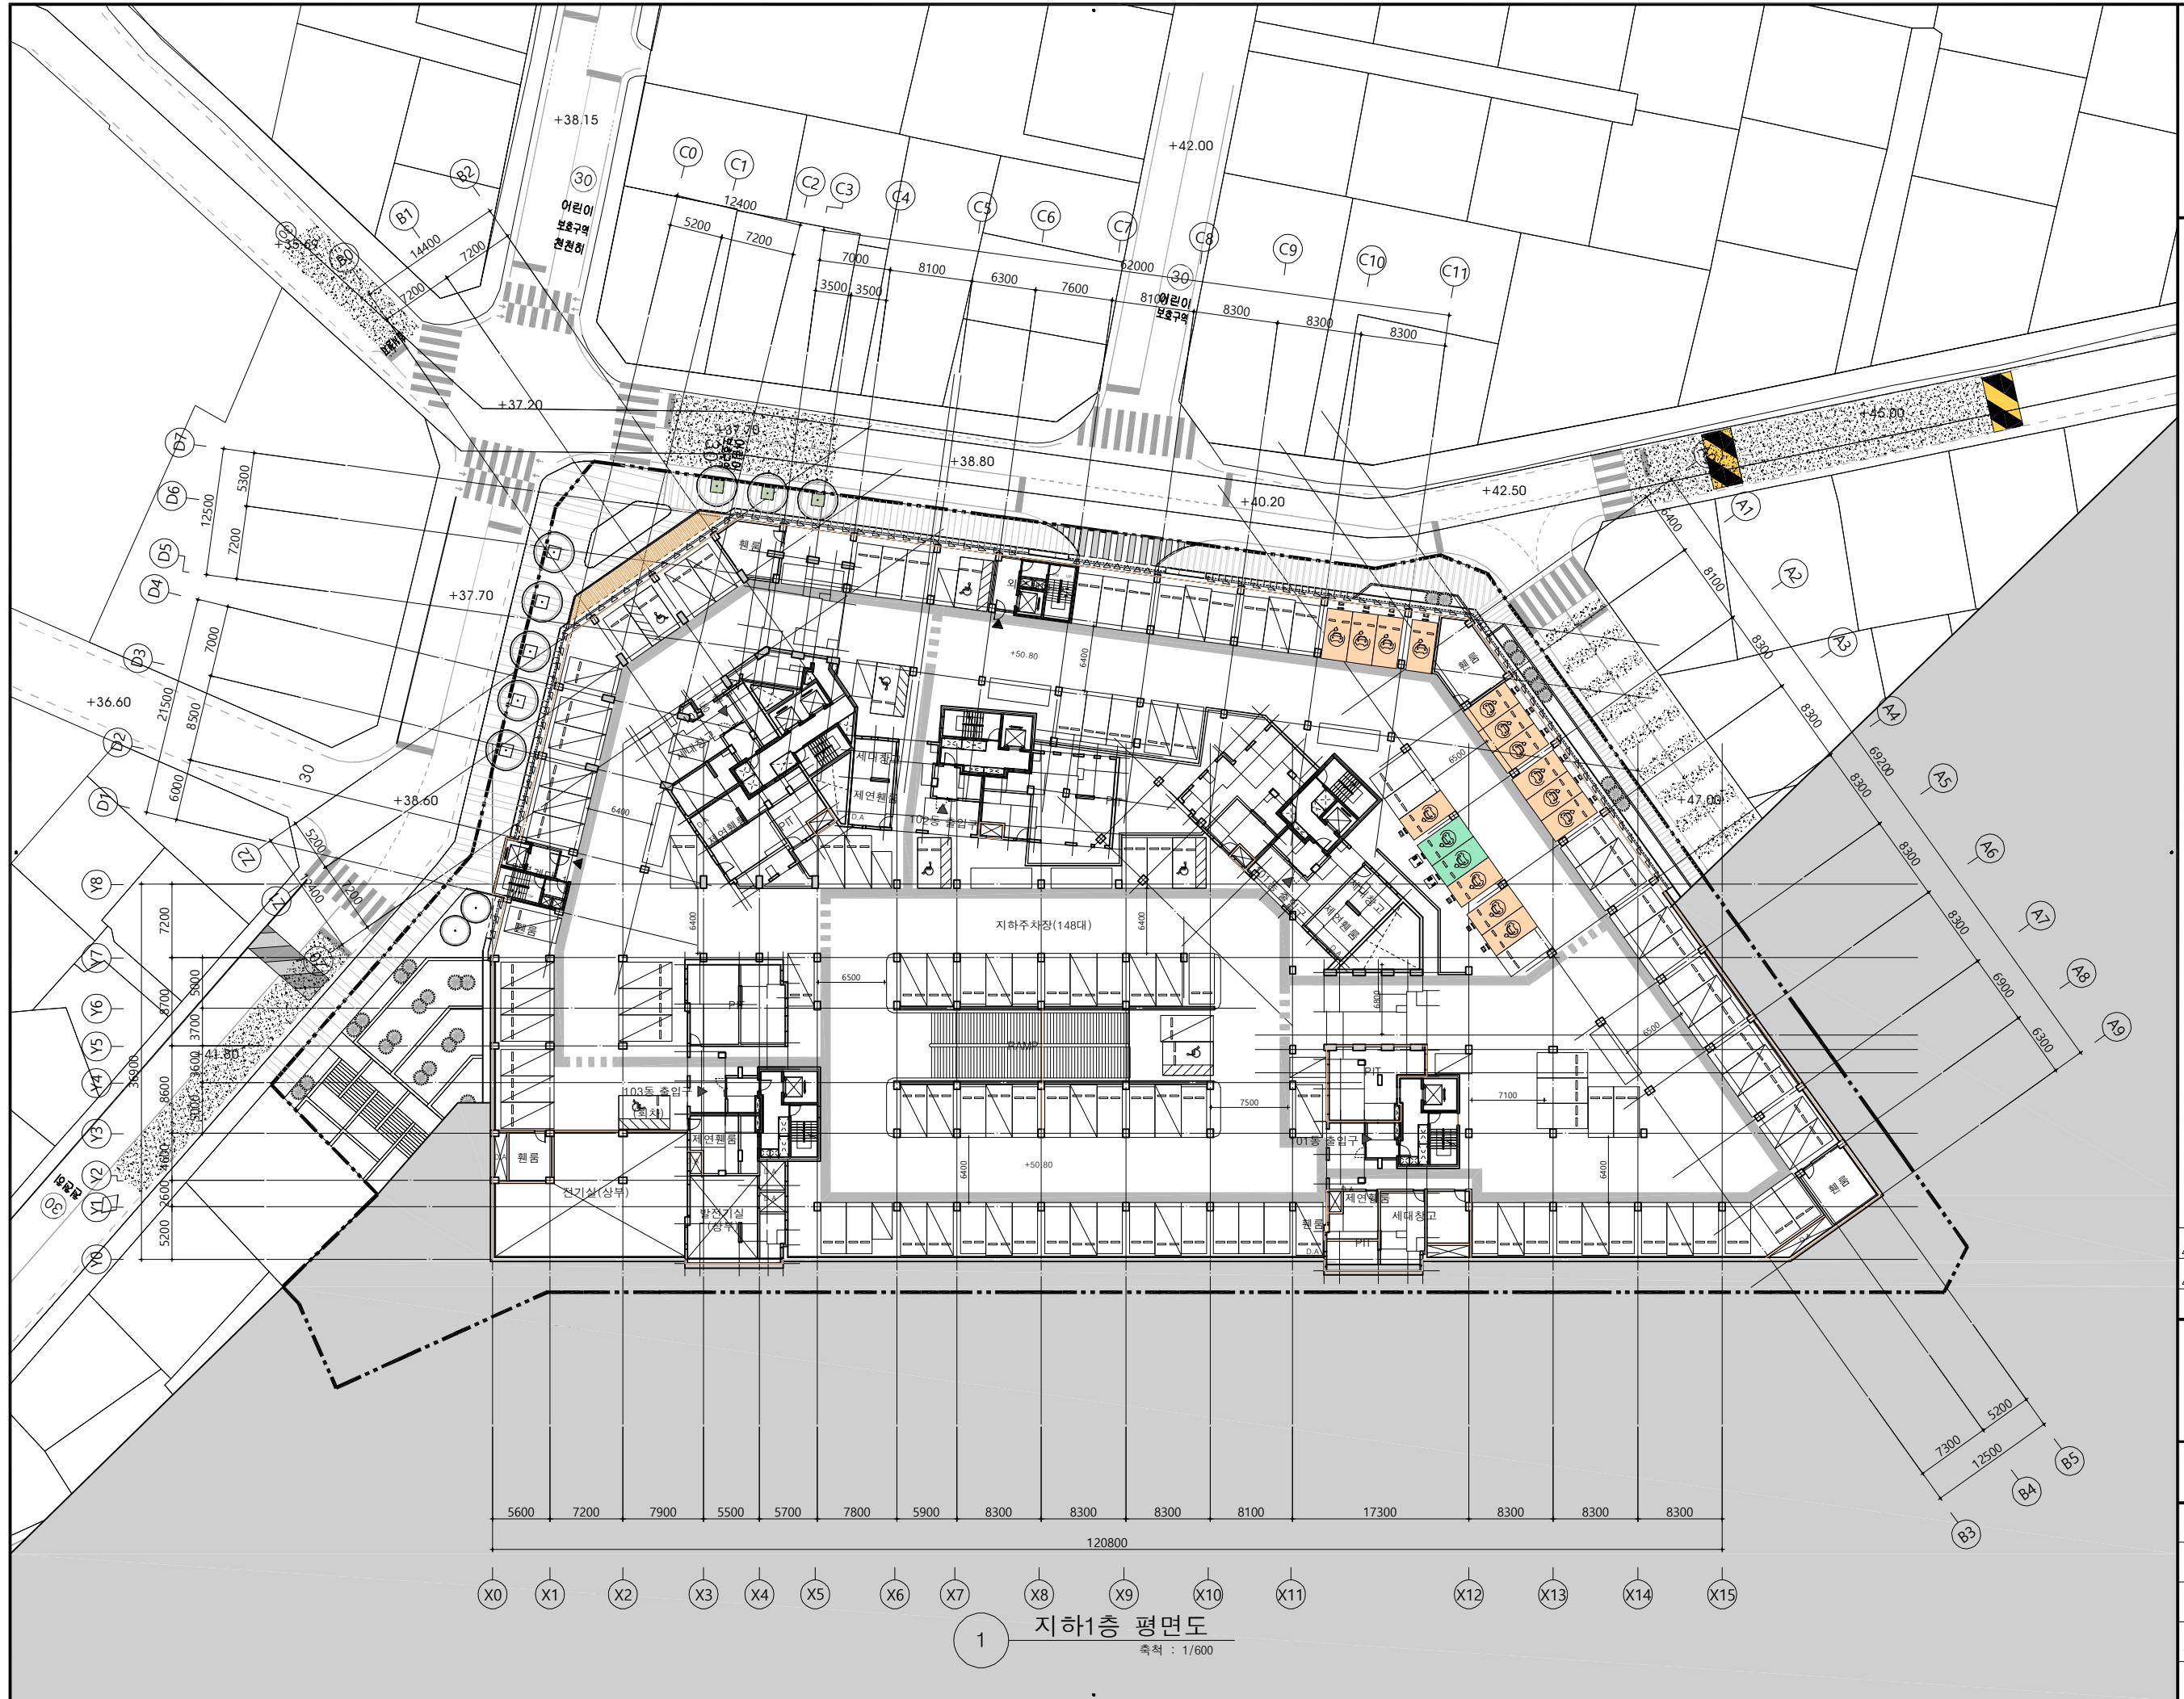

1					
0					
REV.	DATE	DESCRIPTION	BY	BY	APP.

SDglobal

TEL/82-02-6956-9300 SEOUL, KOREA
서울시 성동구 복성로1길 31(성수동1가) 서울을 M타워 308호

DRAWING TITLE

지하1층 평면도

APPROVAL DATE	2025. 07.	APPROVED	
PROJECT NO.		CHECKED 2	
ENGINEER		CHECKED 1	
SCALE	A3: 1/ 600 A1: 1/ 300	DRAWN / DATE	
DRAWING NO.	A-000	REV.	